


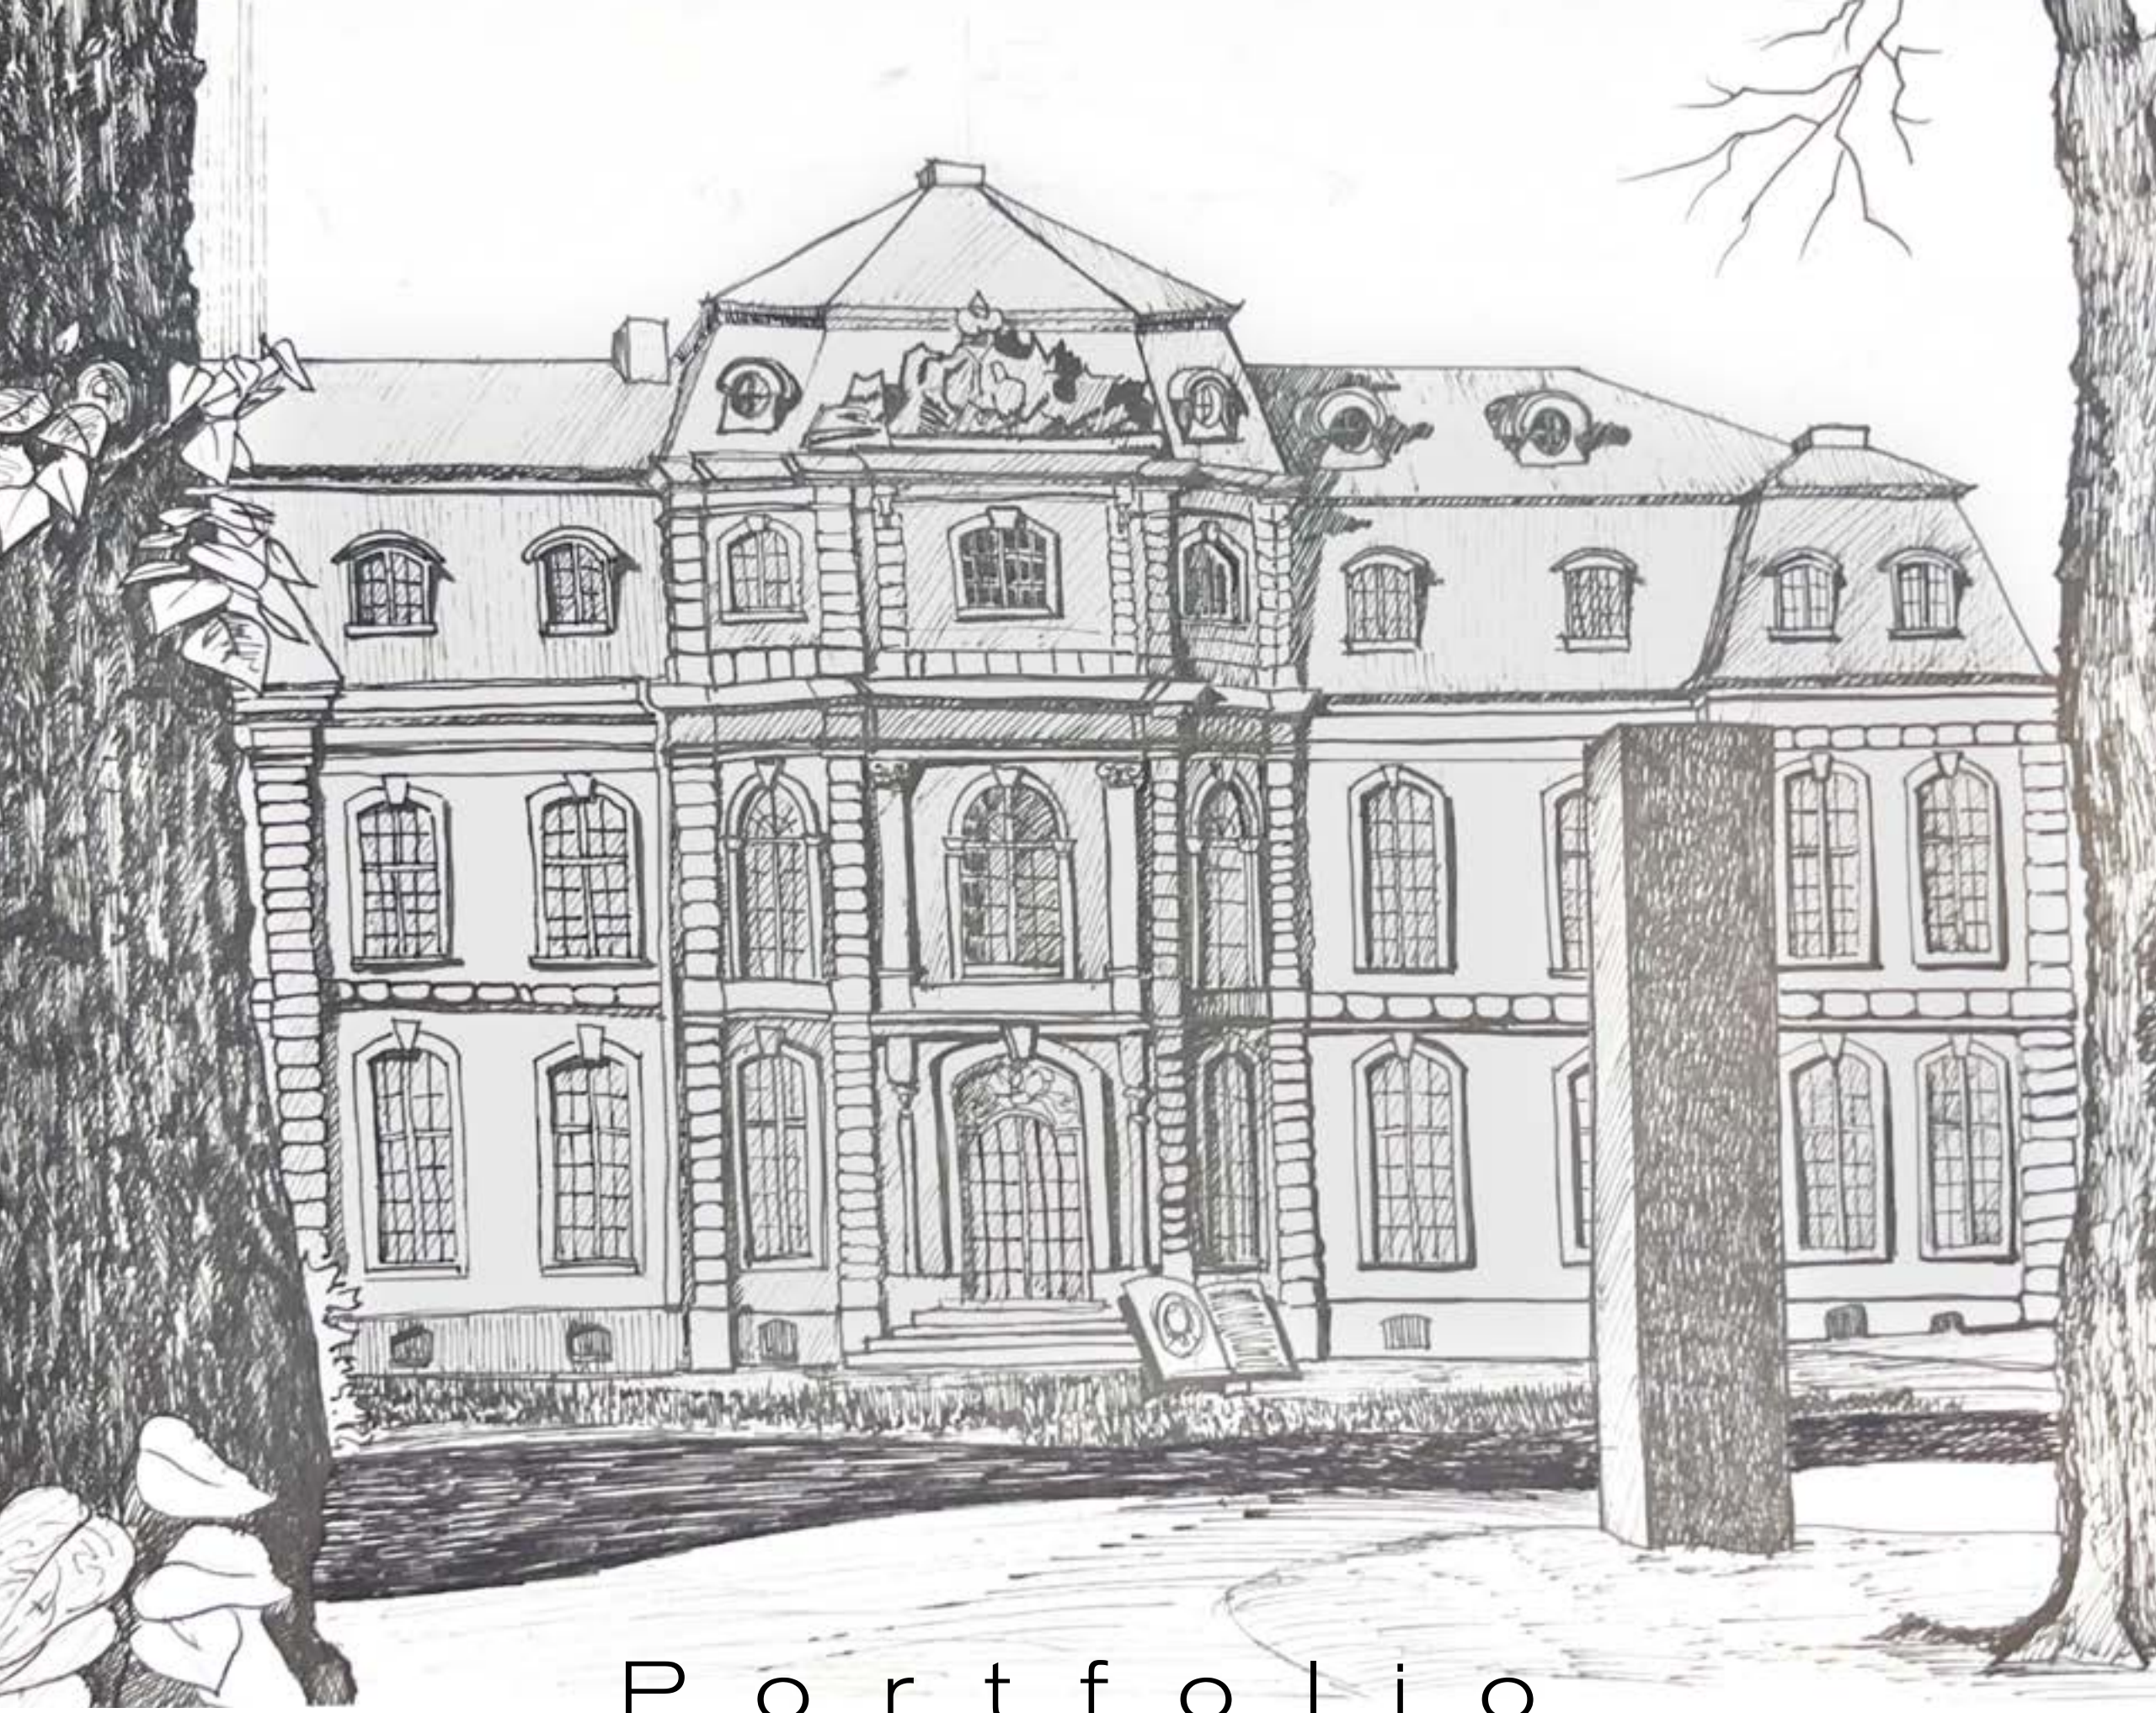

P o r t f o l i o

Architectural work 2020 - 2025

Valeriia Hrynenko

VALERIIA HRYNENKO

hrynenko@umich.edu | 353894034741 | Dublin, IE

As a recent Master of Architecture graduate from Taubman College, I focus on creating design responses that address social needs while balancing stakeholder priorities. My work integrates functional clarity with long-term sustainability, while building expertise in how to support revitalization and future-ready development.

Education

Master of Architecture

Taubman College of Architecture and Planning, University of Michigan | Ann Arbor, MI
05/2025

- Merit Scholarship Recipient (GPA 3.4/4)
- Bridge for Students Scholarship

Bachelor of Arts in Architectural And Building Technology

Kyiv National University of Construction and Architecture | Kyiv, Ukraine
06/2021

- Full Tuition Scholarship and Higher Scholarship Recipient
- Graduated with honors (GPA 3.9/4)

Work Experience

Creator Architect

Archimatika | Kyiv, Ukraine
11/2020 - 05/2021

- **Urban Analysis:** Conducted comprehensive site analysis, evaluating transportation networks, underground features, and land use potential to inform a master planning strategy for the residential complex in Kyiv
- **Strategic Design Thinking:** Developed a strategic design proposal that optimized land use and enhanced site integration, achieved stakeholder approval.
- **Space Planning:** Designed architectural layouts for 20+ apartment units in Odesa, maximized functionality and spatial efficiency
- **Technical Drafting:** Delivered detailed technical drawings for architectural extensions, adhered to budget and material constraints
- **Visual Communication:** Created oral and schematic presentations for project proposals that effectively communicated project designs, which resulted in securing stakeholder approval
- **Team Collaboration:** Optimized cooperation between creating department, team leader and landscape team

Skills

Design and Technical Software:

- Advanced: Revit 2025, Photoshop, InDesign,
- Intermediate: Excel, Dynamo, Rhino, Enscape, AutoCAD
- Basic: SketchUp, Energy Plus

Design and Drawing Skills:

- Conceptual visualization (styled and collaged)
- Schematic design and space planning,
- Precise technical drafting

Analytical:

- Site and environmental analysis, space planning,
- Historical and cultural research, community engagement,
- Building life cycle and material analysis, and structural analysis

Interpersonal:

- Creative problem-solving with structured thinking
- Active listening, empathy, and collaborative communication
- Systemic creativity,
- Consistent detail delivery,
- Efficient resource and time management, adherence to deadlines.

Languages: Ukrainian (native), English (fluent)

Competitions

REbuild Ukraine Competition

Canada and Ukraine | 08/2023

- **Modular Design Thinking:** Proposed a post-war mass housing solution using prefabricated systems focused on adaptability, speed, and cost-efficiency.
- **Material Research:** Explored sustainable materials for environmentally conscious housing solutions.
- **Urban Strategy:** Addressed urban integration, community needs, and scalability to ensure functional and inclusive design.

She Builds Ukraine Hackathon

Canada, Ukraine | 06/2023

- **Team Leadership and Coordination:** Led a team of 4 undergraduate students in designing an AI-powered debris sorting system, emphasizing sustainable reconstruction practices.
- **Awards:** Secured 7th place out of 40 for optimized resource use and environmental impact reduction in post-conflict reconstruction.

STEELFREEDOM National Competition

Mariupol, Ukraine | 11/2020

- **Leadership:** Led a team of 4 in designing a stadium.
- **Awards:** Achieved a top 10 finalist position out of 60 teams for innovative use of steel tree-columns, structural clarity, and efficient land use.

Additional Experience

Fundraiser

Office of Development, University of Michigan Telefund | Ann Arbor, MI
01/2024 - 04/2025

- **Negotiation and Consistency:** fundraised over \$15,000 for UofM funds, regularly contributing 10–30% of shift campaign totals through persistent and respectful outreach.
- **Trust and Autonomy:** Promoted to Authorized Fundraiser within one semester for consistently high performance, trusted to confirm pledges and process transactions without managerial oversight.

Car Creative Photographer

AutoFocus | Austin, TX
03/2023 – 07/2023

- **Workflow Efficiency:** Photographed 15-20 cars daily, ensuring on-time update to the company website.
- **Attention to Detail:** Promoted from Chevrolet to Infinity photography within 2 months, reflecting consistent performance and attention to detail.

Youth Camp Manager/Tutor

Plast, Ukrainian Scouts | Valencia, Spain
07/2022 - 08/2022

- **Adaptability and Leadership:** Managed logistics and activity planning in a fast-paced camp environment; tutored displaced children with empathy and structure.

Humanitarian Aid Coordinator

Plast | Valencia, Spain
02/2022 - 04/2022

- **Process Optimization:** Transformed sorting and packaging of humanitarian aid into a conveyor-line process.

English Tutor

AIESEC | Levico Terme, Italy
07/2019 - 08/2019

- **Curriculum Design:** Led educational sessions for underserved youth across two locations, independently planning and delivering age-appropriate English activities.

Environmental Conservation Assistant

“Extremal” Camp | Korostyshiv, Ukraine
15/10/2019

- **Environmental Stewardship:** Cleaned the area of 50m² of forest at the Quarry of Korostyshev to facilitate a site for outdoor mountaineering activities.

“Work and Travel” Program

Server, Dave & Buster's | Jacksonville, FL
05/2018 - 08/2018

Gained experience in customer service, time management, and multitasking in a high-pressure setting.

Publication: BUILD MASTER CLASS Conference | Kyiv, Ukraine

10/2017

Presented paper “The Manipulation of the ‘Kyivan Rus’ Narrative in Politics Through Architecture”.

Contents

01 Reconstruction

2023. The competition project focused on modernizing standardized prefabricated housing using concrete modules.
pages 1-4

02 KinoStep

2024. Architectural sequel, that brought Italian Casa Malaparte to the streets of Ann Arbor, Michigan.
pages 7-10


03 MUSEUM

2021. Bachelor's diploma inspired by Renzo Piano's approach of managing urban vibrancy.
pages 11-14

04 Stadium


2020. National competition award-winning project showcases the freedom of steel.
pages 15-18

01 Reconstruction of Panel Housing
Microregion Analysis

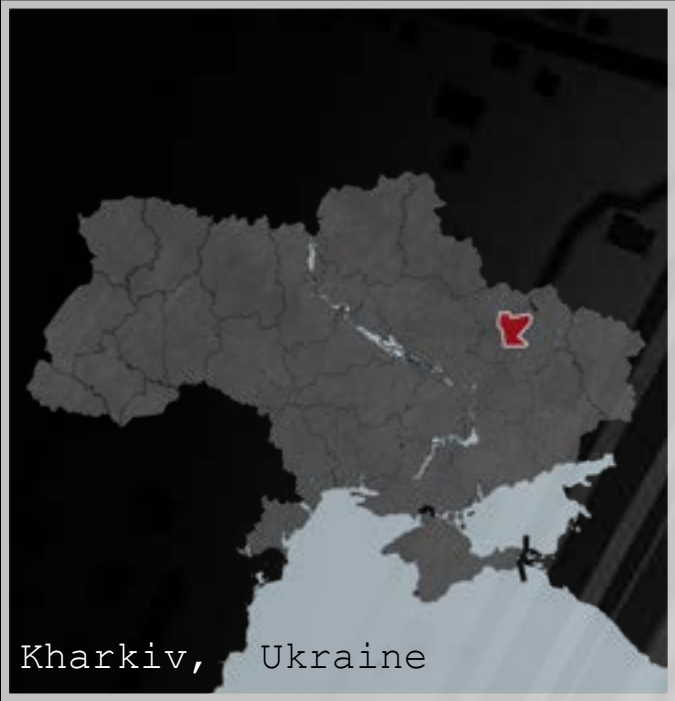



1. Seizure unreliable panels

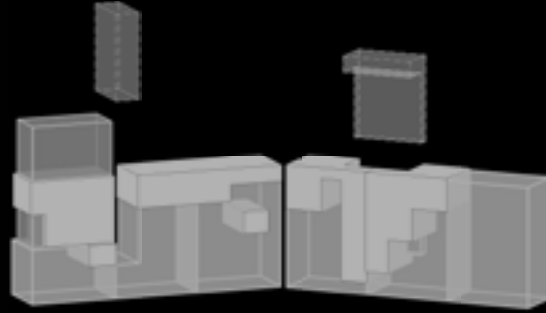

2. Defining mass blocks



3. Adding dynamics to the silhouette

Buildings are damaged in the district




Damage done to a residential 9 story building.
Address: 78 Uzhviy St, Kharkiv

01 Reconstruction




The competition was centered around the integration of **prefabricated modules** into standardized grid of series 11-7 to experiment with **silhouette** and **program rethinking** under **streamlined restoration**

O1 Reconstruction of Panel Housing
Structural Details

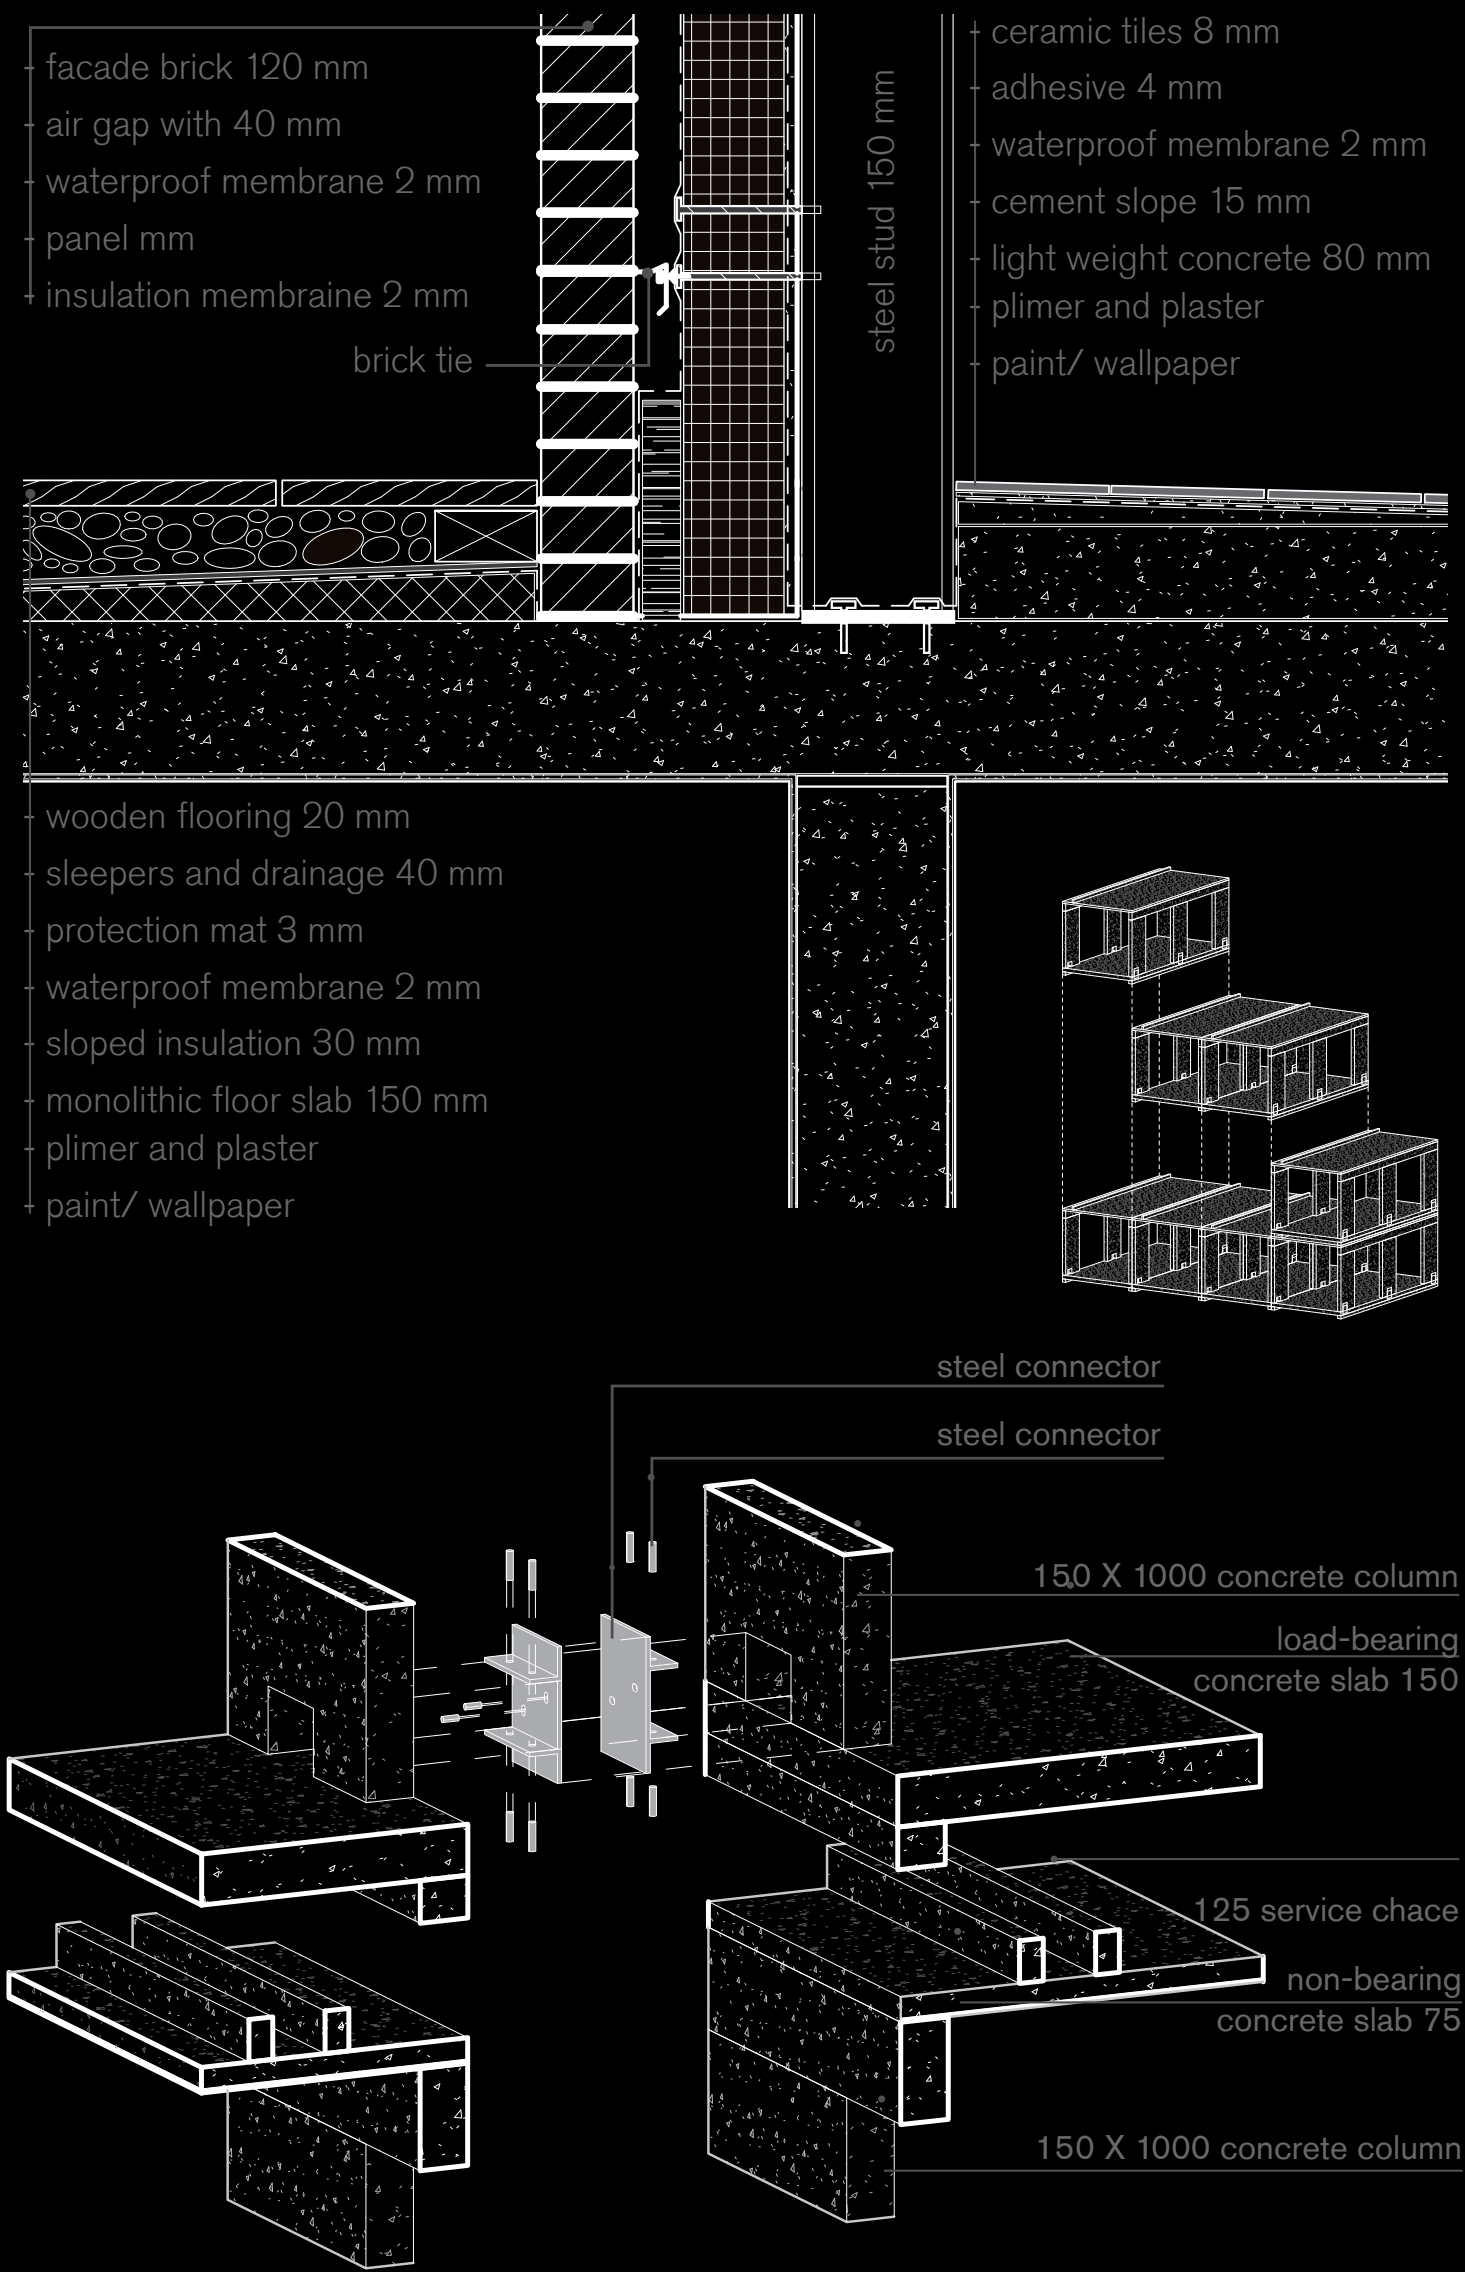


01 Reconstruction of Panel Housing



Module Fitting

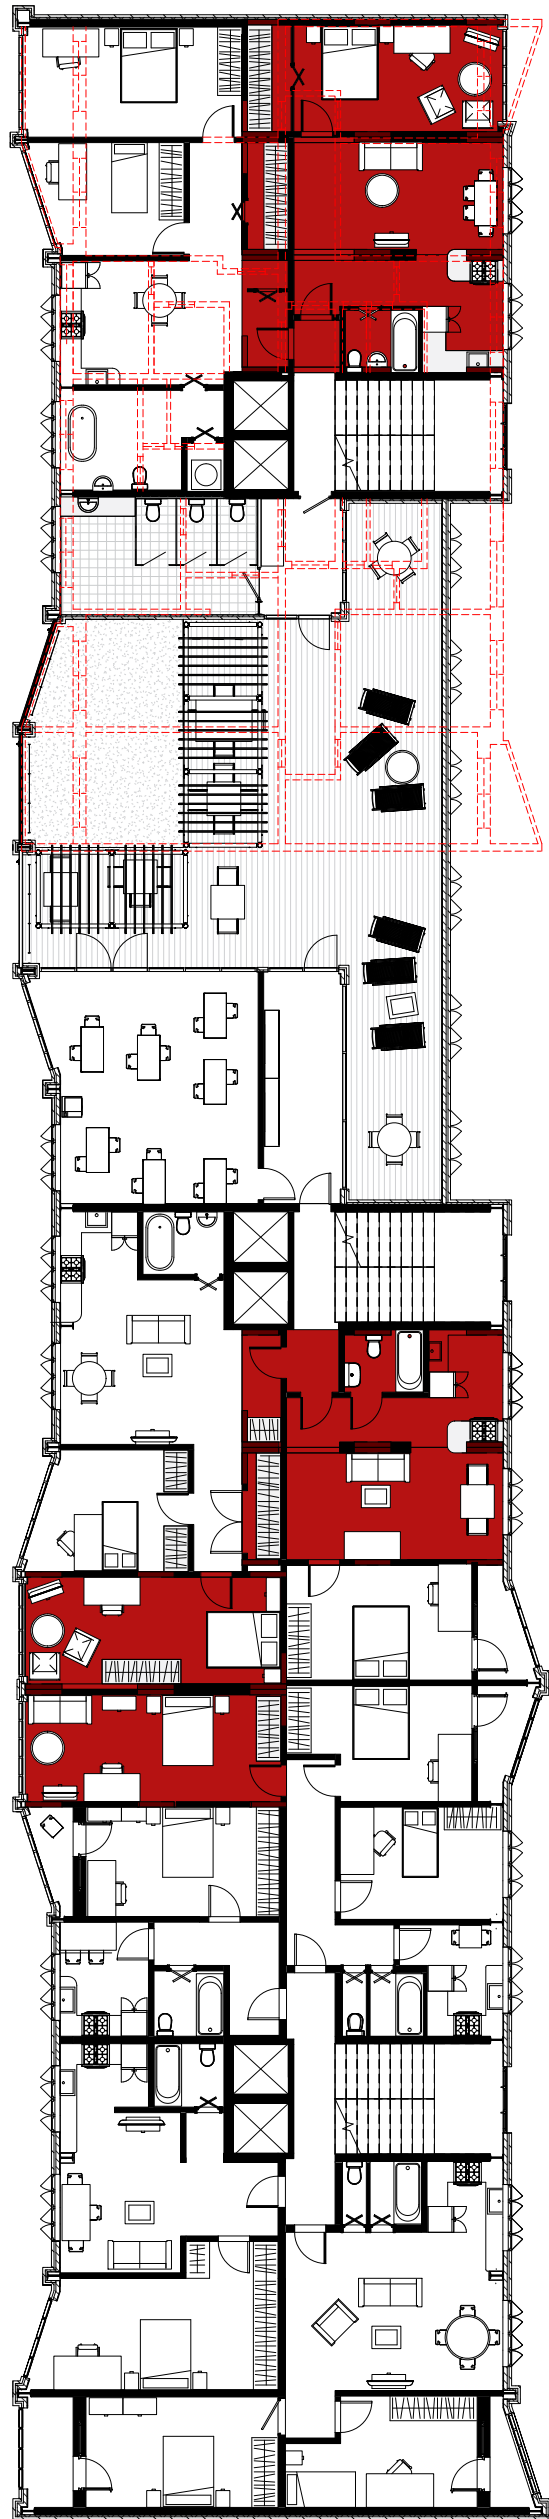

O2 Nature and Science Museum
Site Analysis

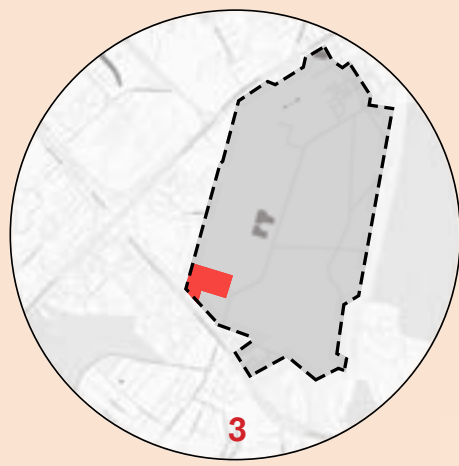

[1] The capital of Ukraine is facing a transitional period reflecting historic political and economic changes. [2] In the peripheral district of Kyiv, [3] the site lies within a large area registered as state property and includes an underused Soviet-era exhibition complex surrounded by forest. [4] Soviet housing defines the area's higher population density and identifies families and students as the primary users.

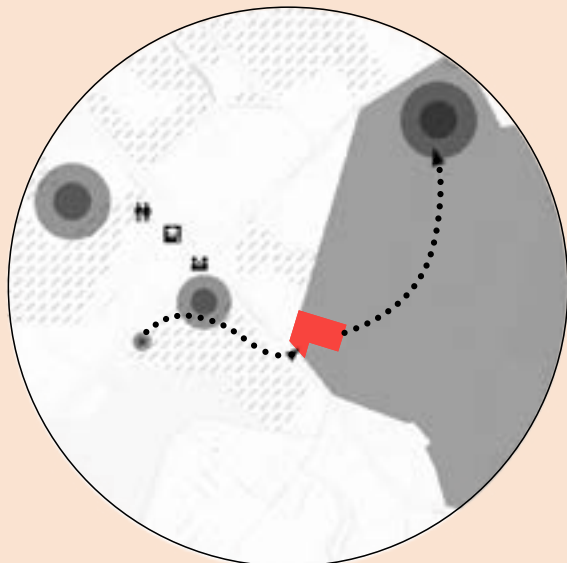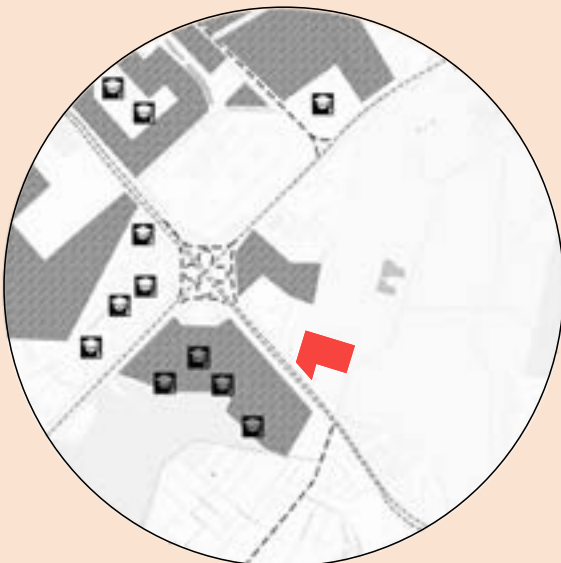

[5] The proposal aims to balance limited public infrastructure and [6] offer a transition between urban and outdoor leisure zones.

[7] Despite mild urban decay, the transportation network secures the site connection to the rest of Kyiv with bus routes and metro. Nearby bus stops and pedestrian access highlight the site's walkability.

garden of water



outdoor theater

library entrance

employee parking

bus parking

guest parking

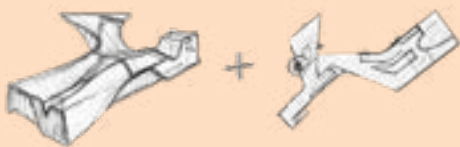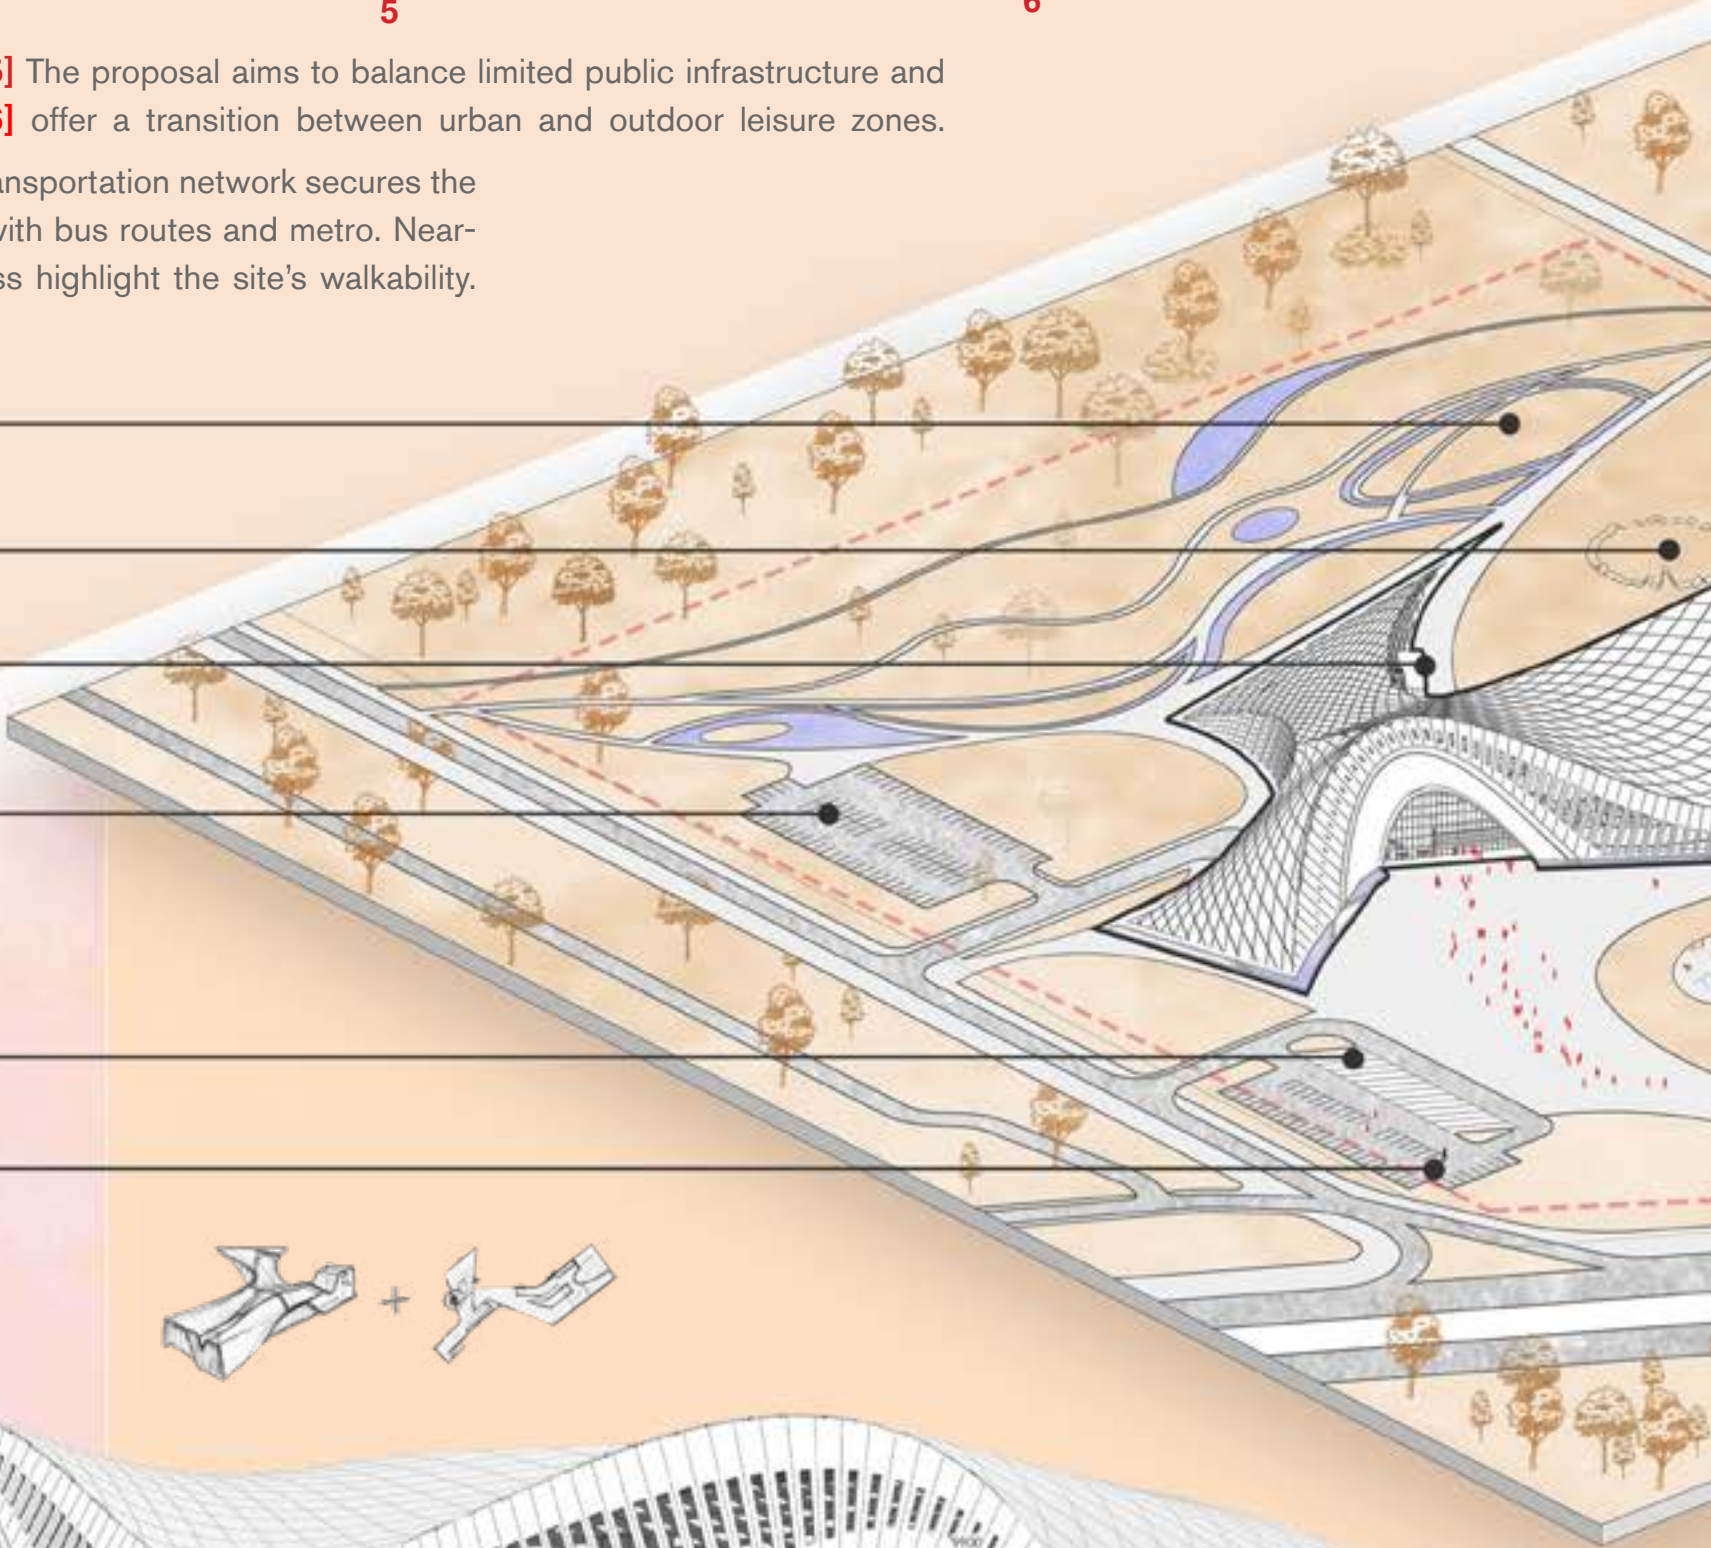



O2 MUSEUM




football pitch

basketball pitch


playground

main entrance

O1 Reconstruction of Panel Housing
Envelope

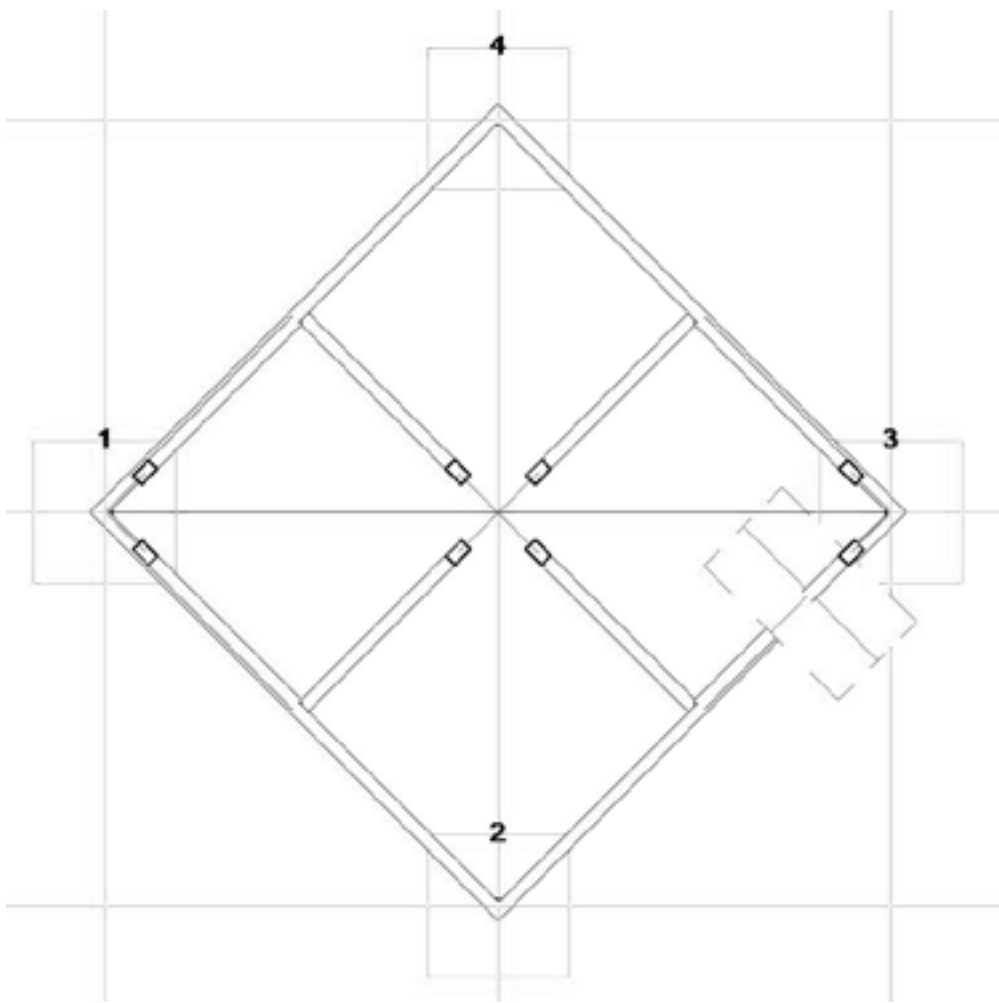




The parametric dome spans several independent volumes, including a museum, library, and restaurant, each containing their own support spaces. The voids between these structures act as transitional zones that generate much-needed third spaces. The envelope, constructed from adaptive lightweight steel modules with polycarbonate panels, provides high light transmission while keeping the need for stabilizing interior temperatures. Modules are prefabricated off-site and assembled on-site using bolted connections and lightweight cranes.

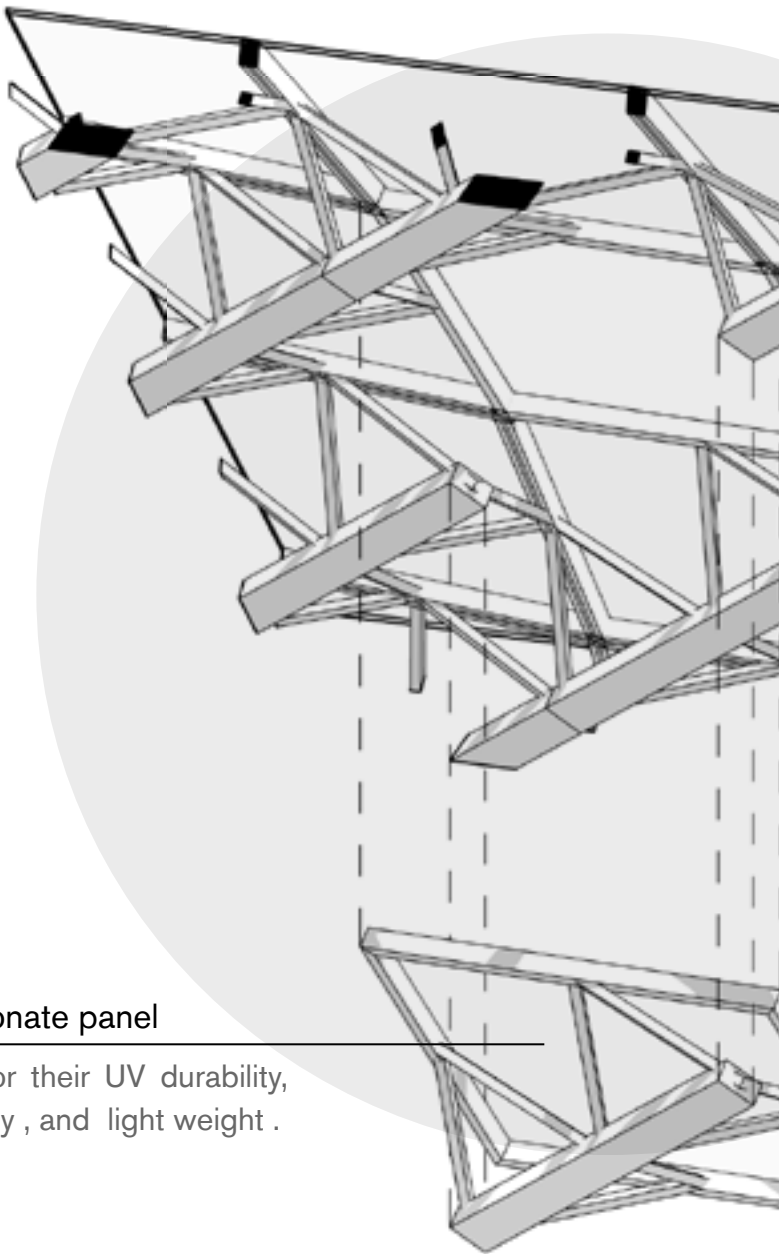

Polycarbonate panel

Chosen for their UV durability, affordability , and light weight .

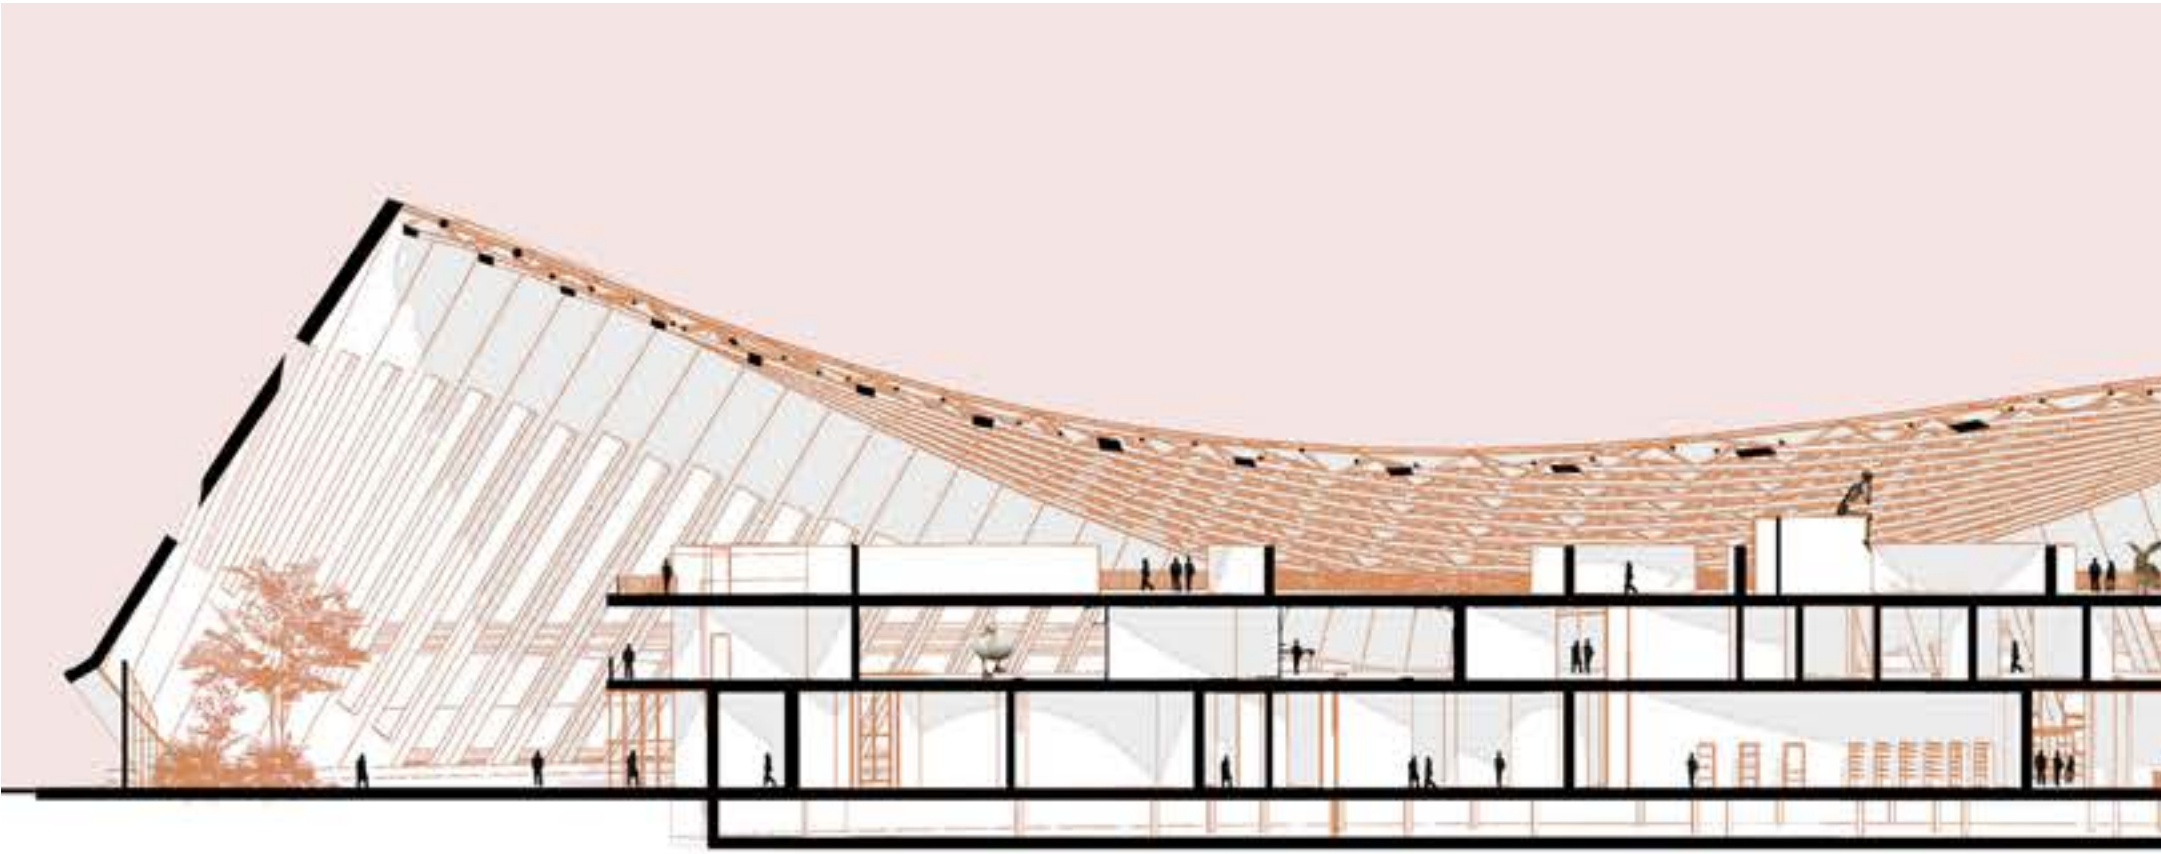

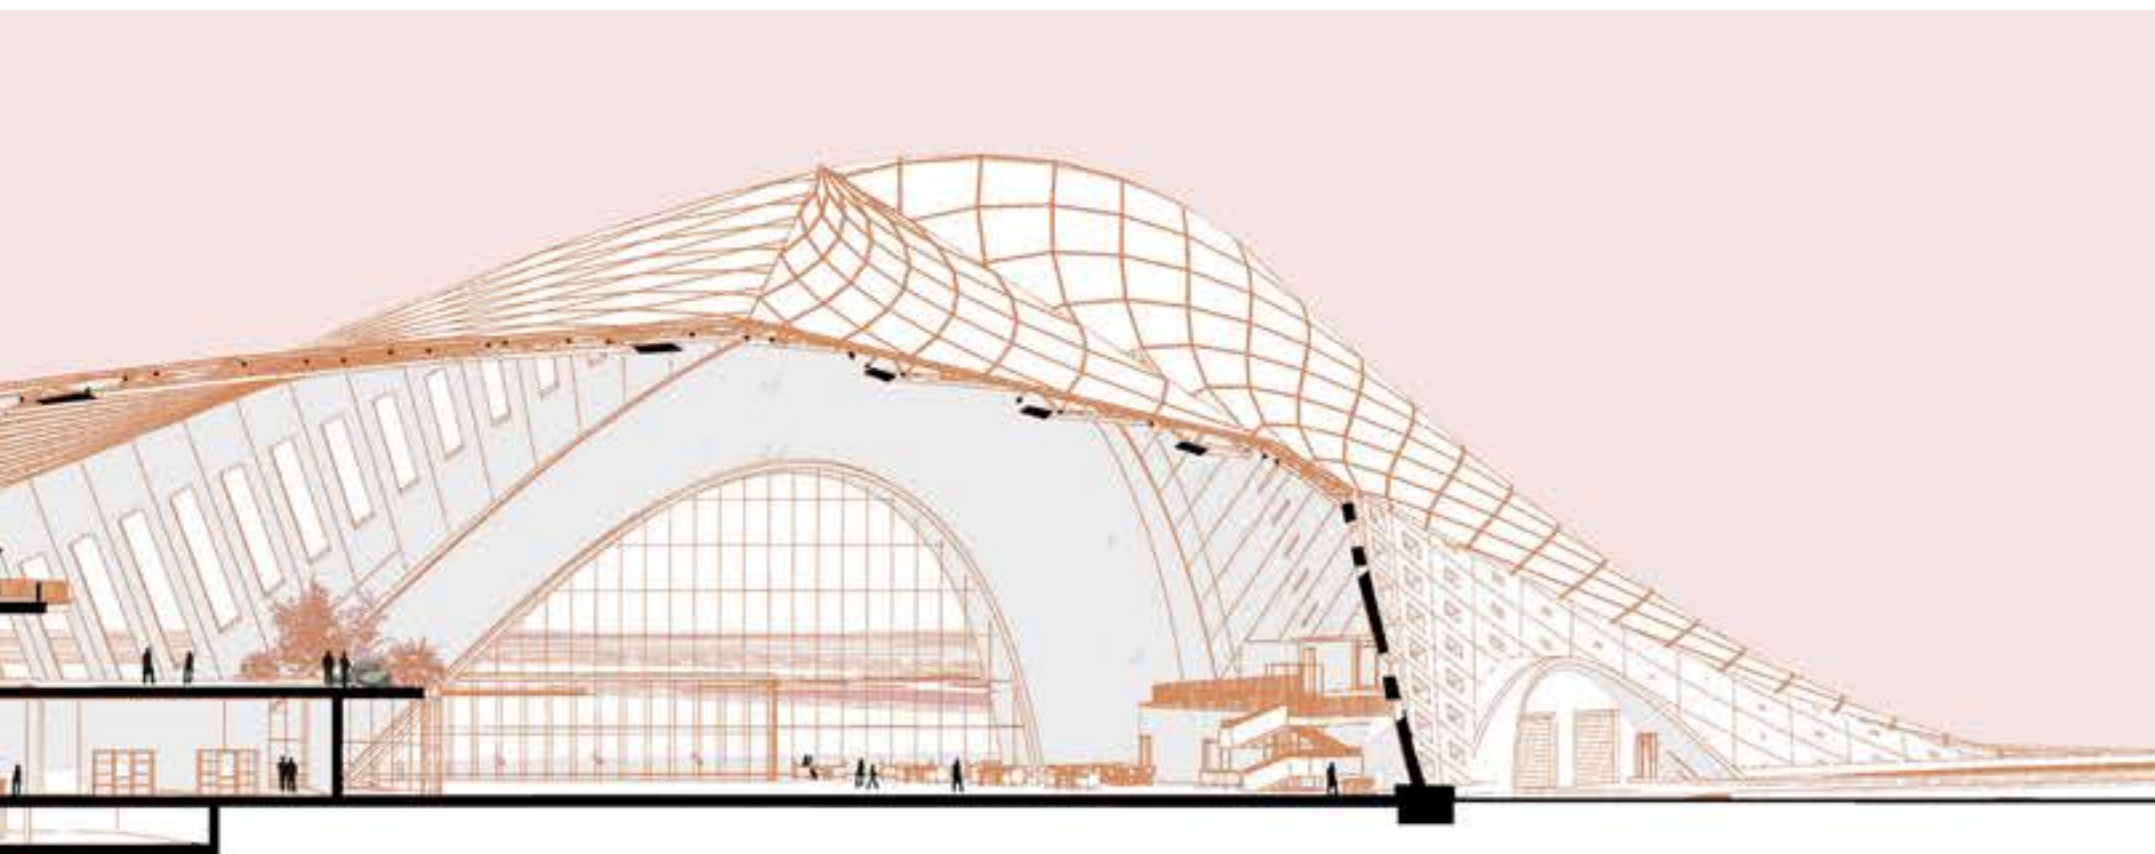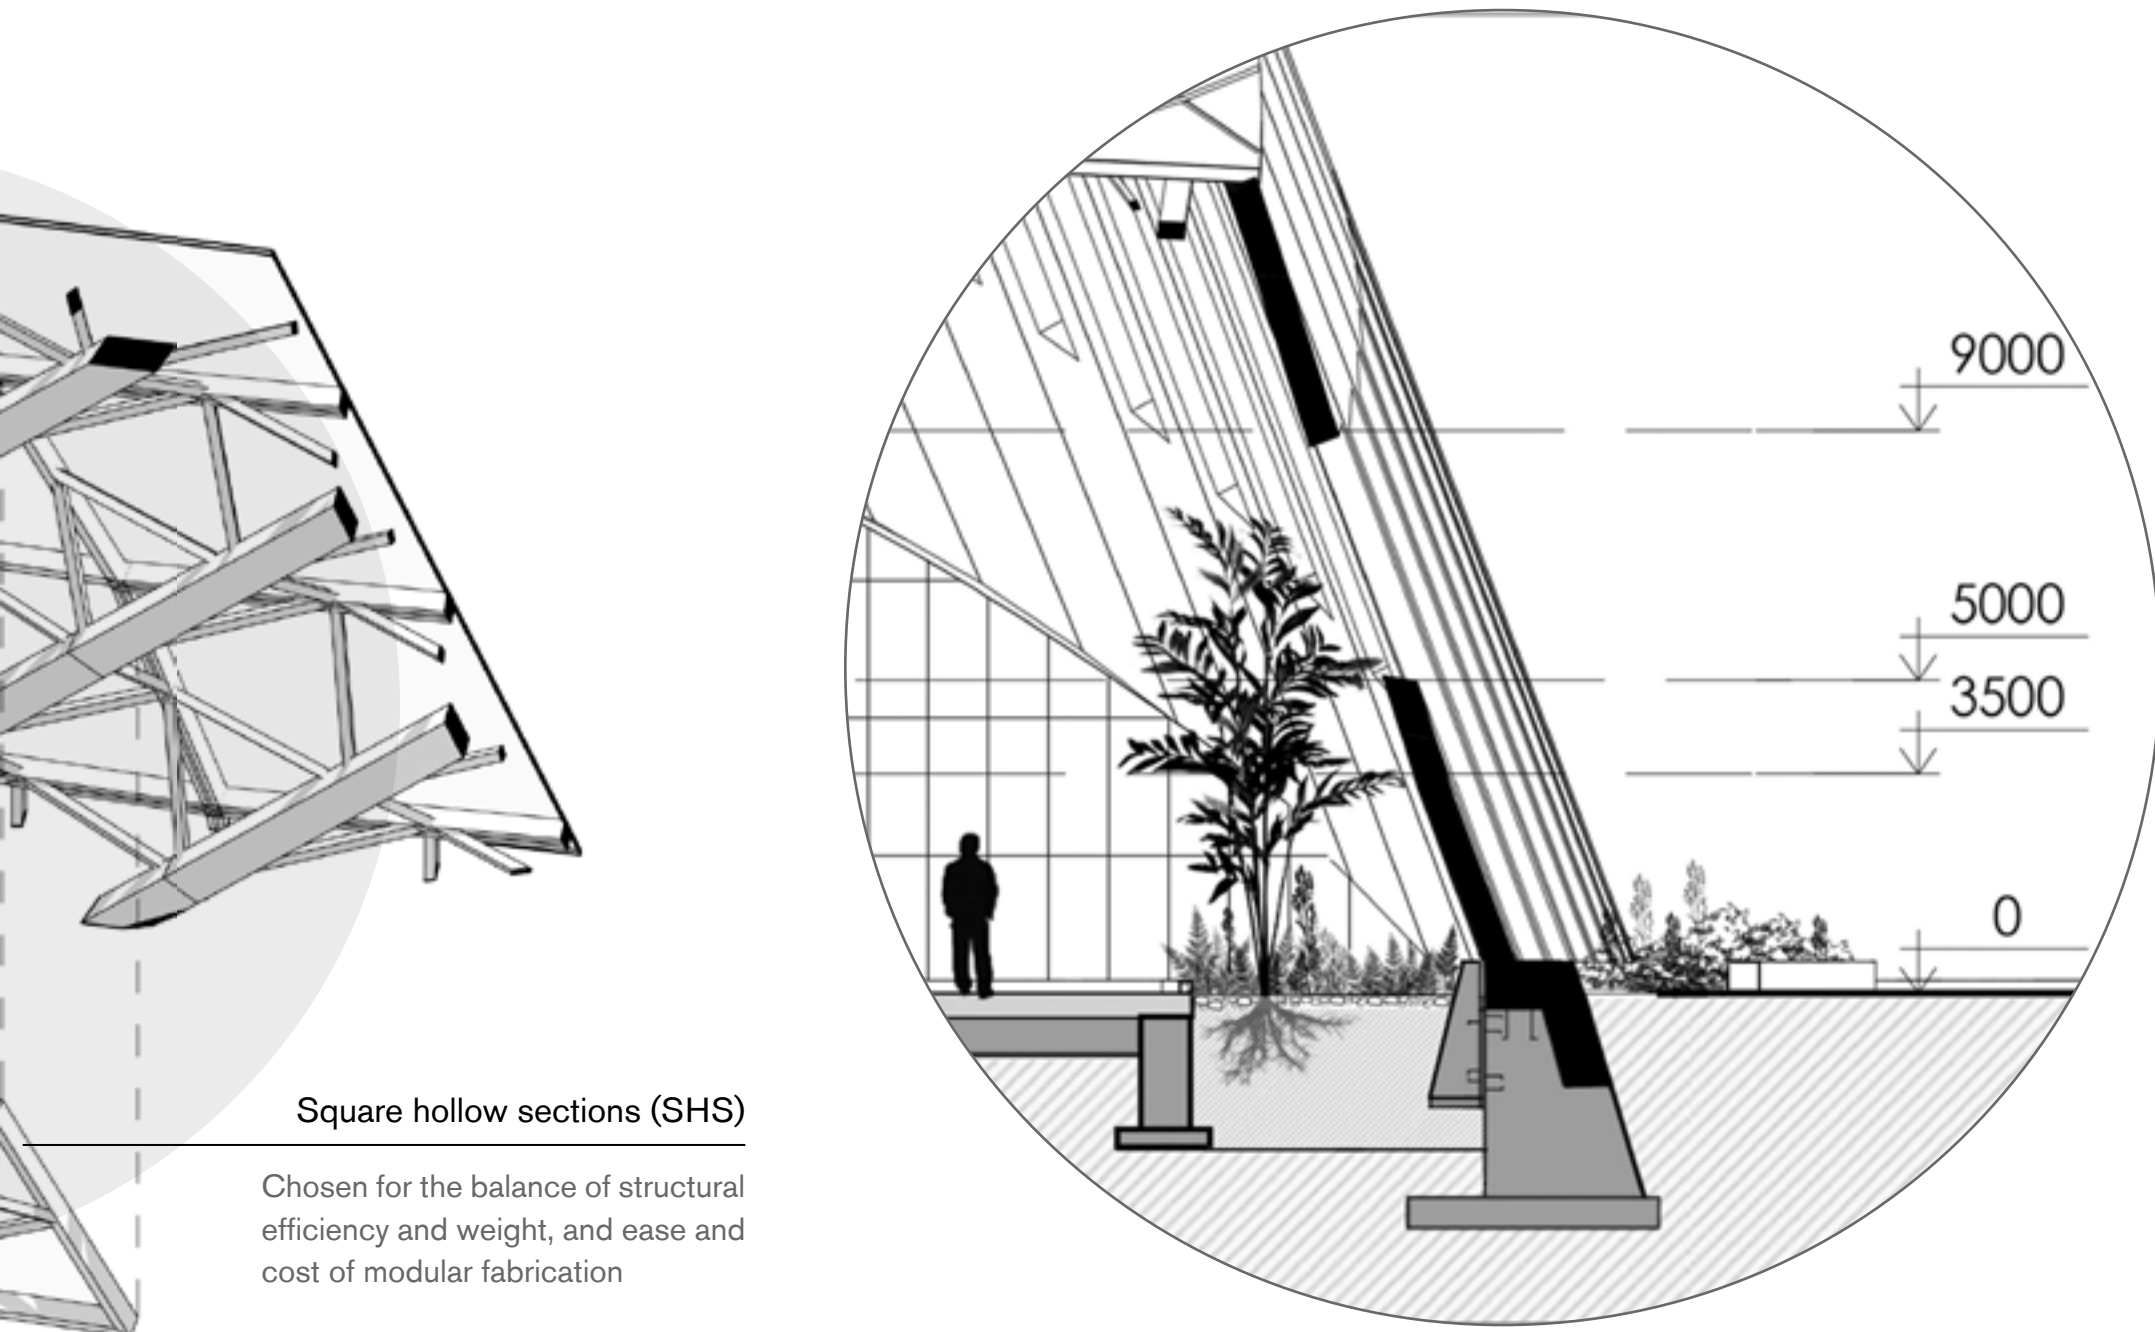



03 Casa Malaparte to KinoStep

Sequel Studio challenged me to design a conceptual continuation to an existing architectural landmark. Specil logic, material or structure - anything could become a leading motif in the new inspiration.



Ann Arbor YMCA

W Washington St

Second St



Liberty
Anne

W William St

Burnt Toast Inn

The Egyptian Theatre as a precedent study


Its design combines features of traditional theater and modern cinema. Spatial experiences it provides through form, vision, ornament, and color stands out as dramatic as functional. The programmatic layering offers a dynamic sequence of spaces that guide visitors from gathering zones to intimate performance areas.

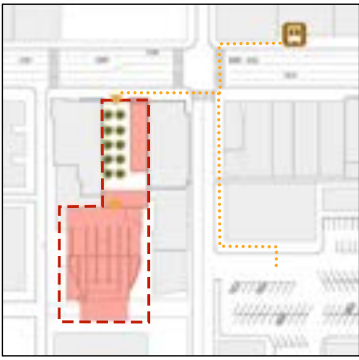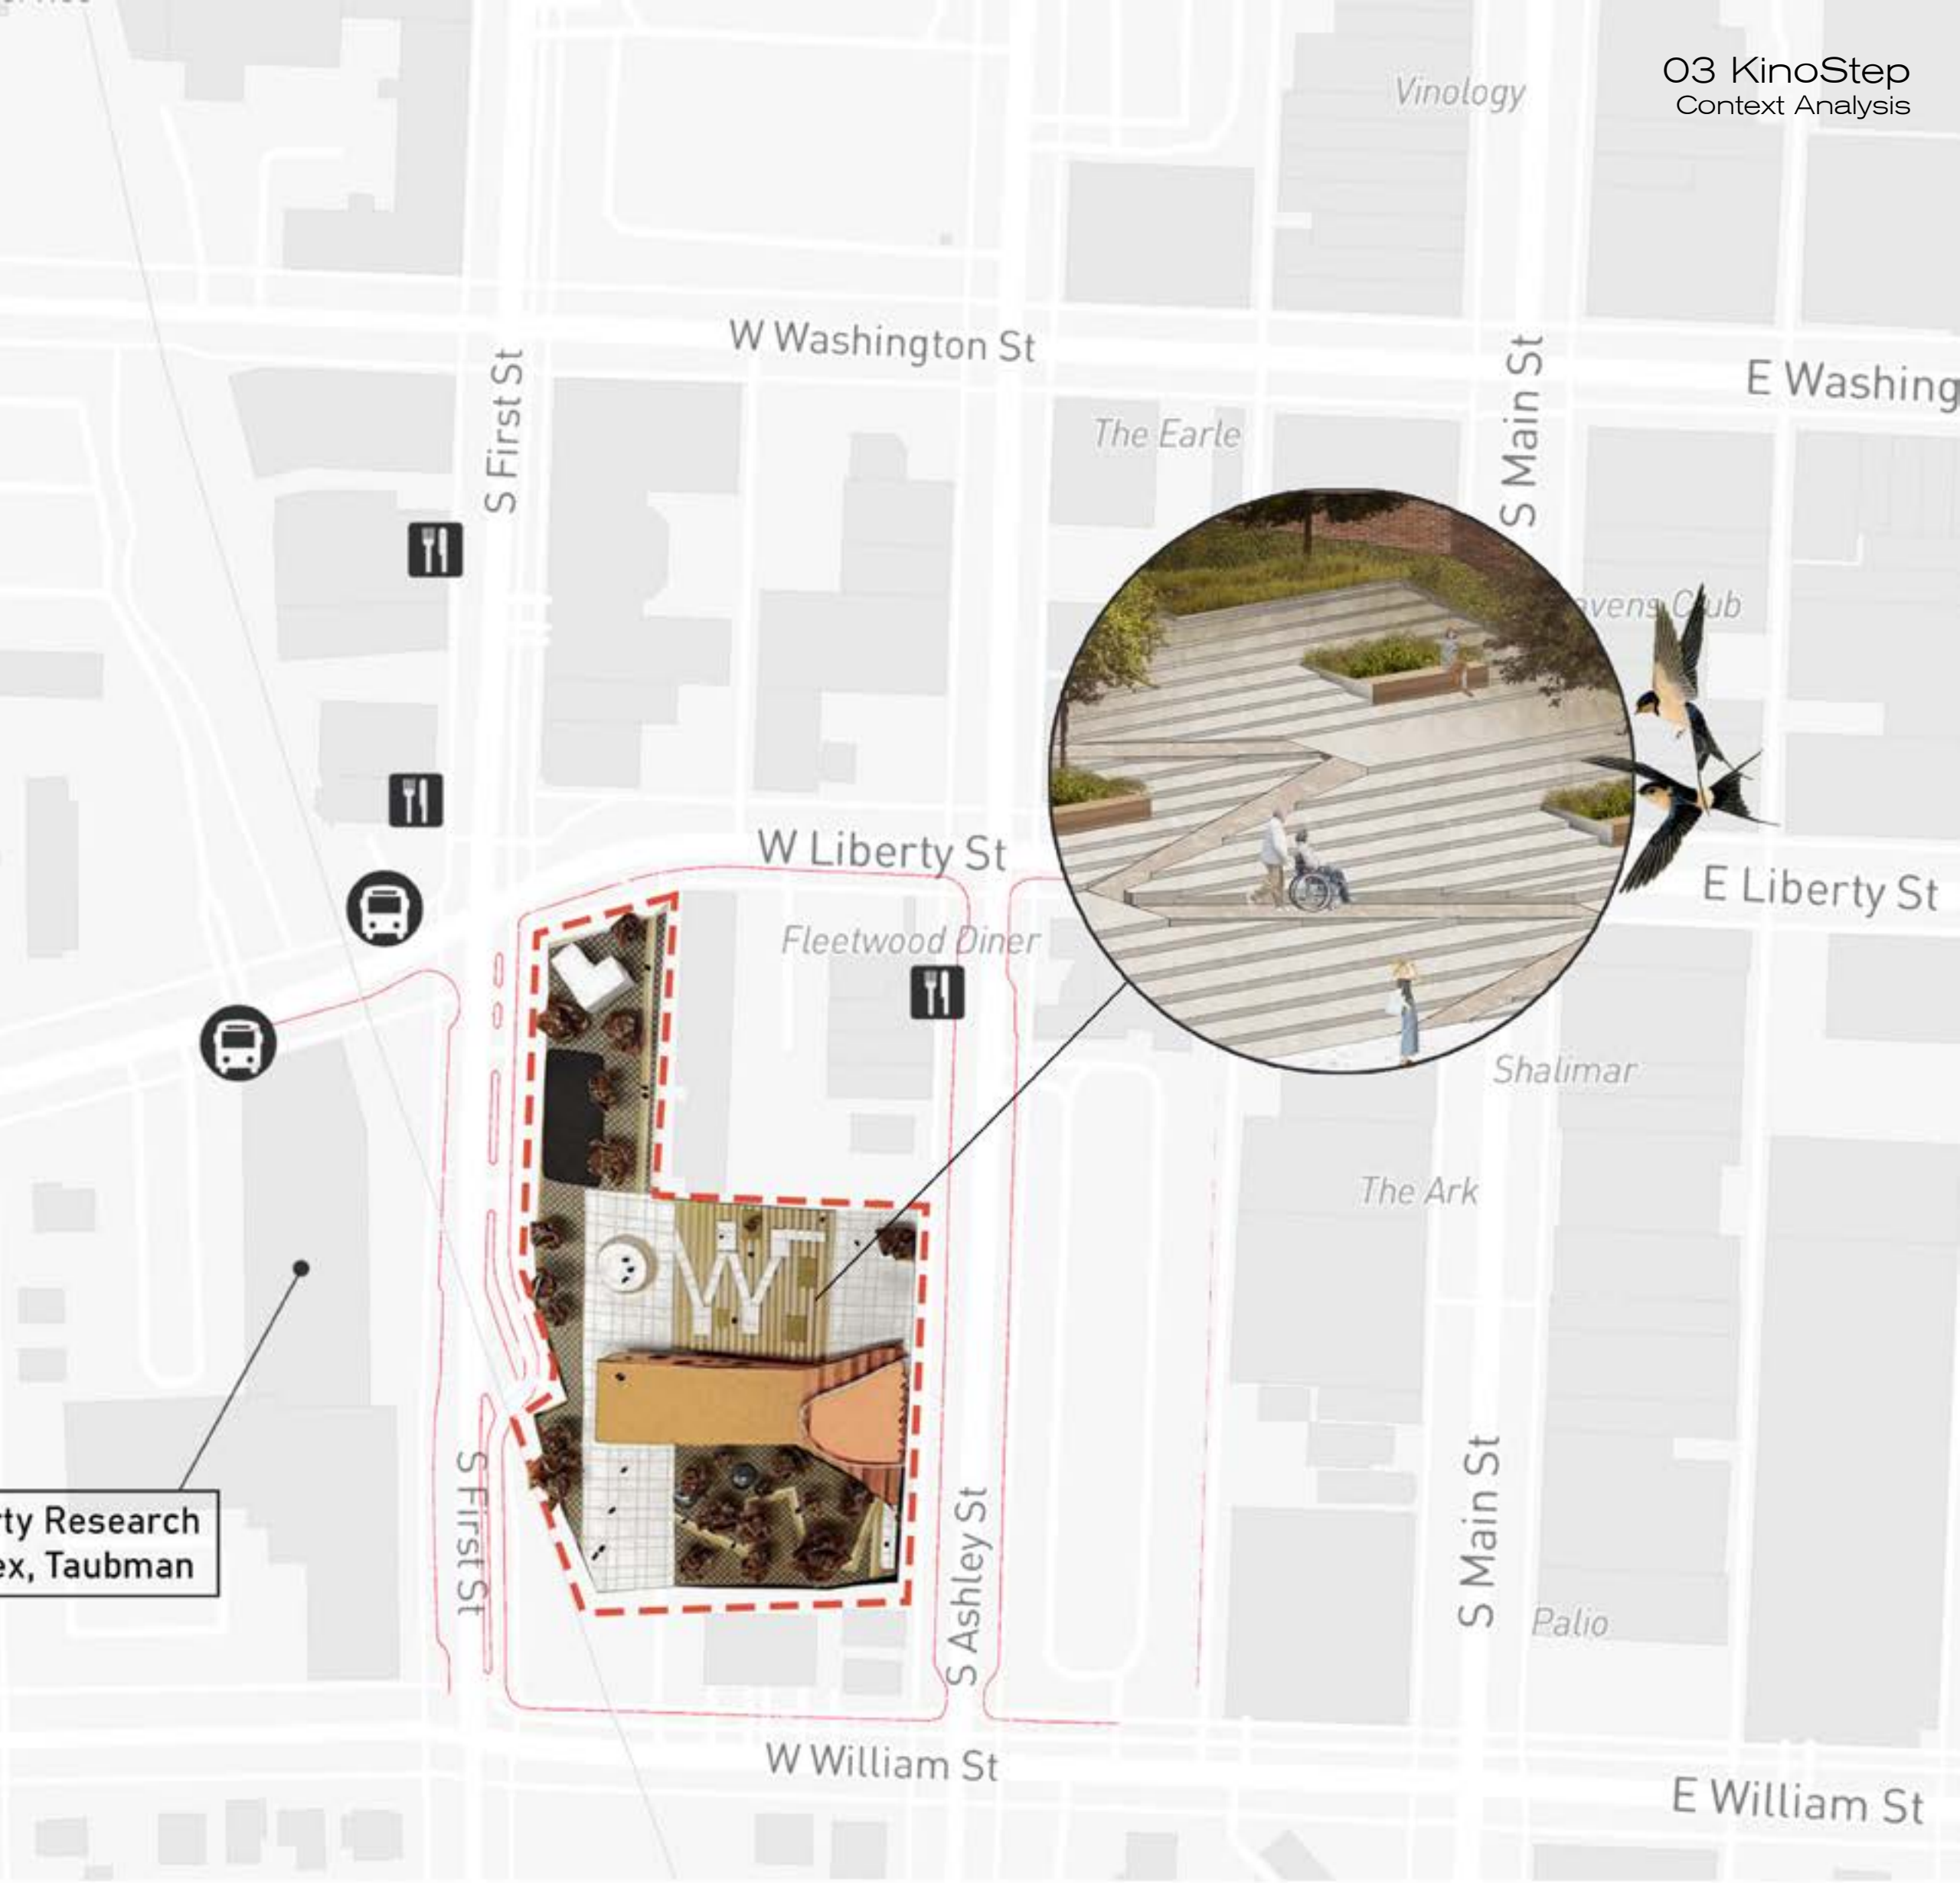

Site accessibility



Spatial massing

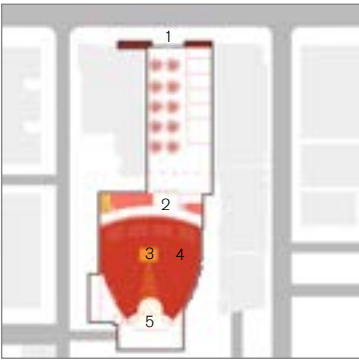

Program

1- entrance, 2- foyer, 3 - booth,
4 - auditorium, 5 - screen.



Spatial hierarchy



Interior

04 KinoStep
Section








The KinoStep building creates two distinct architectural expressions on each side. A great console extends above a spacious plaza observing the transitional space below. On the other side, the dynamic facade continues the existing rhythm of street view.



Program legend:

- Observation deck
- Lobby
- Circulation
- Retail
- Auditorium
- Screening rooms
- Bar
- Office, storage
- Restrooms

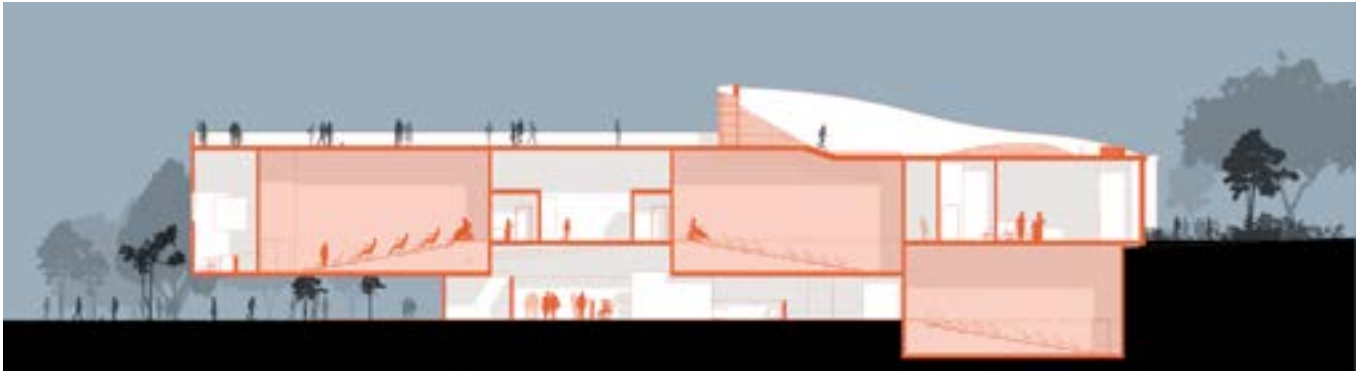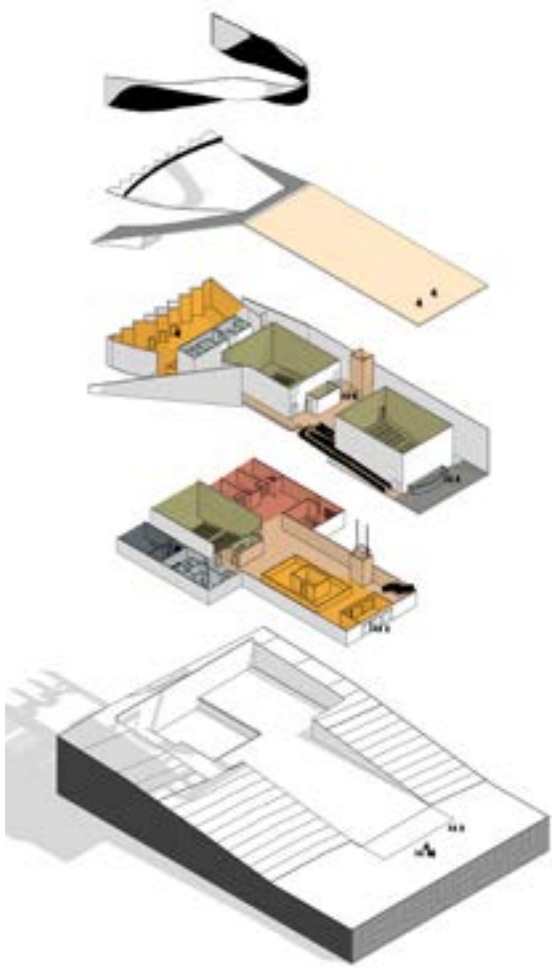

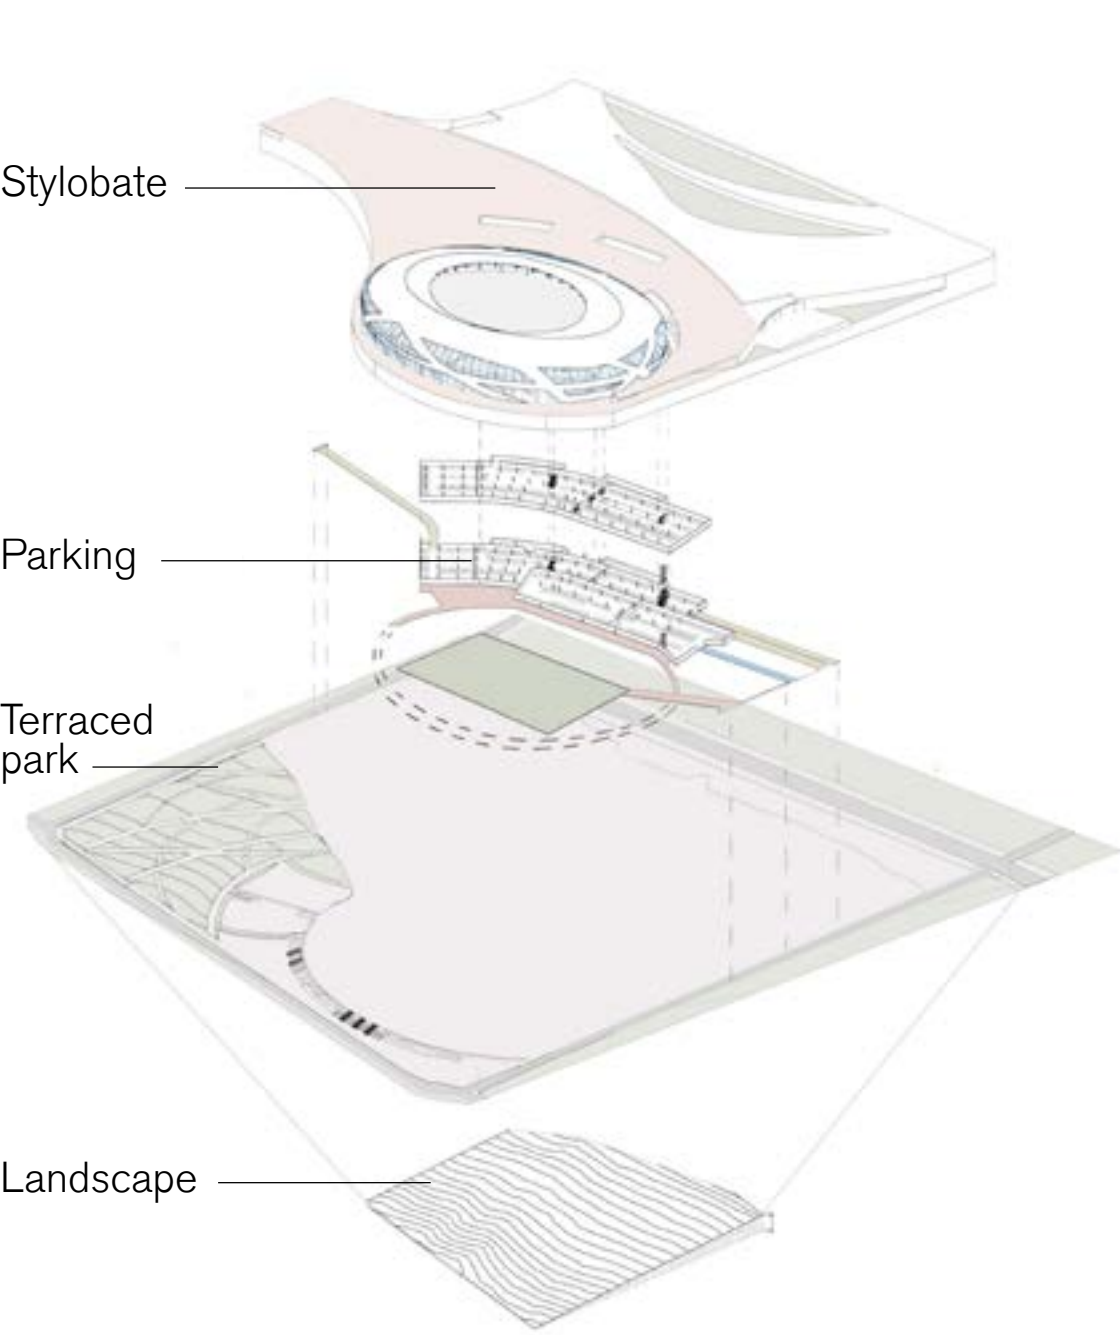

The site features an 11-meter-high slope, which accommodates an underground parking covered with a stylobate. The parking is connected to the road on both sides of the site. This creates a spacious public square above while concealing the parking below.

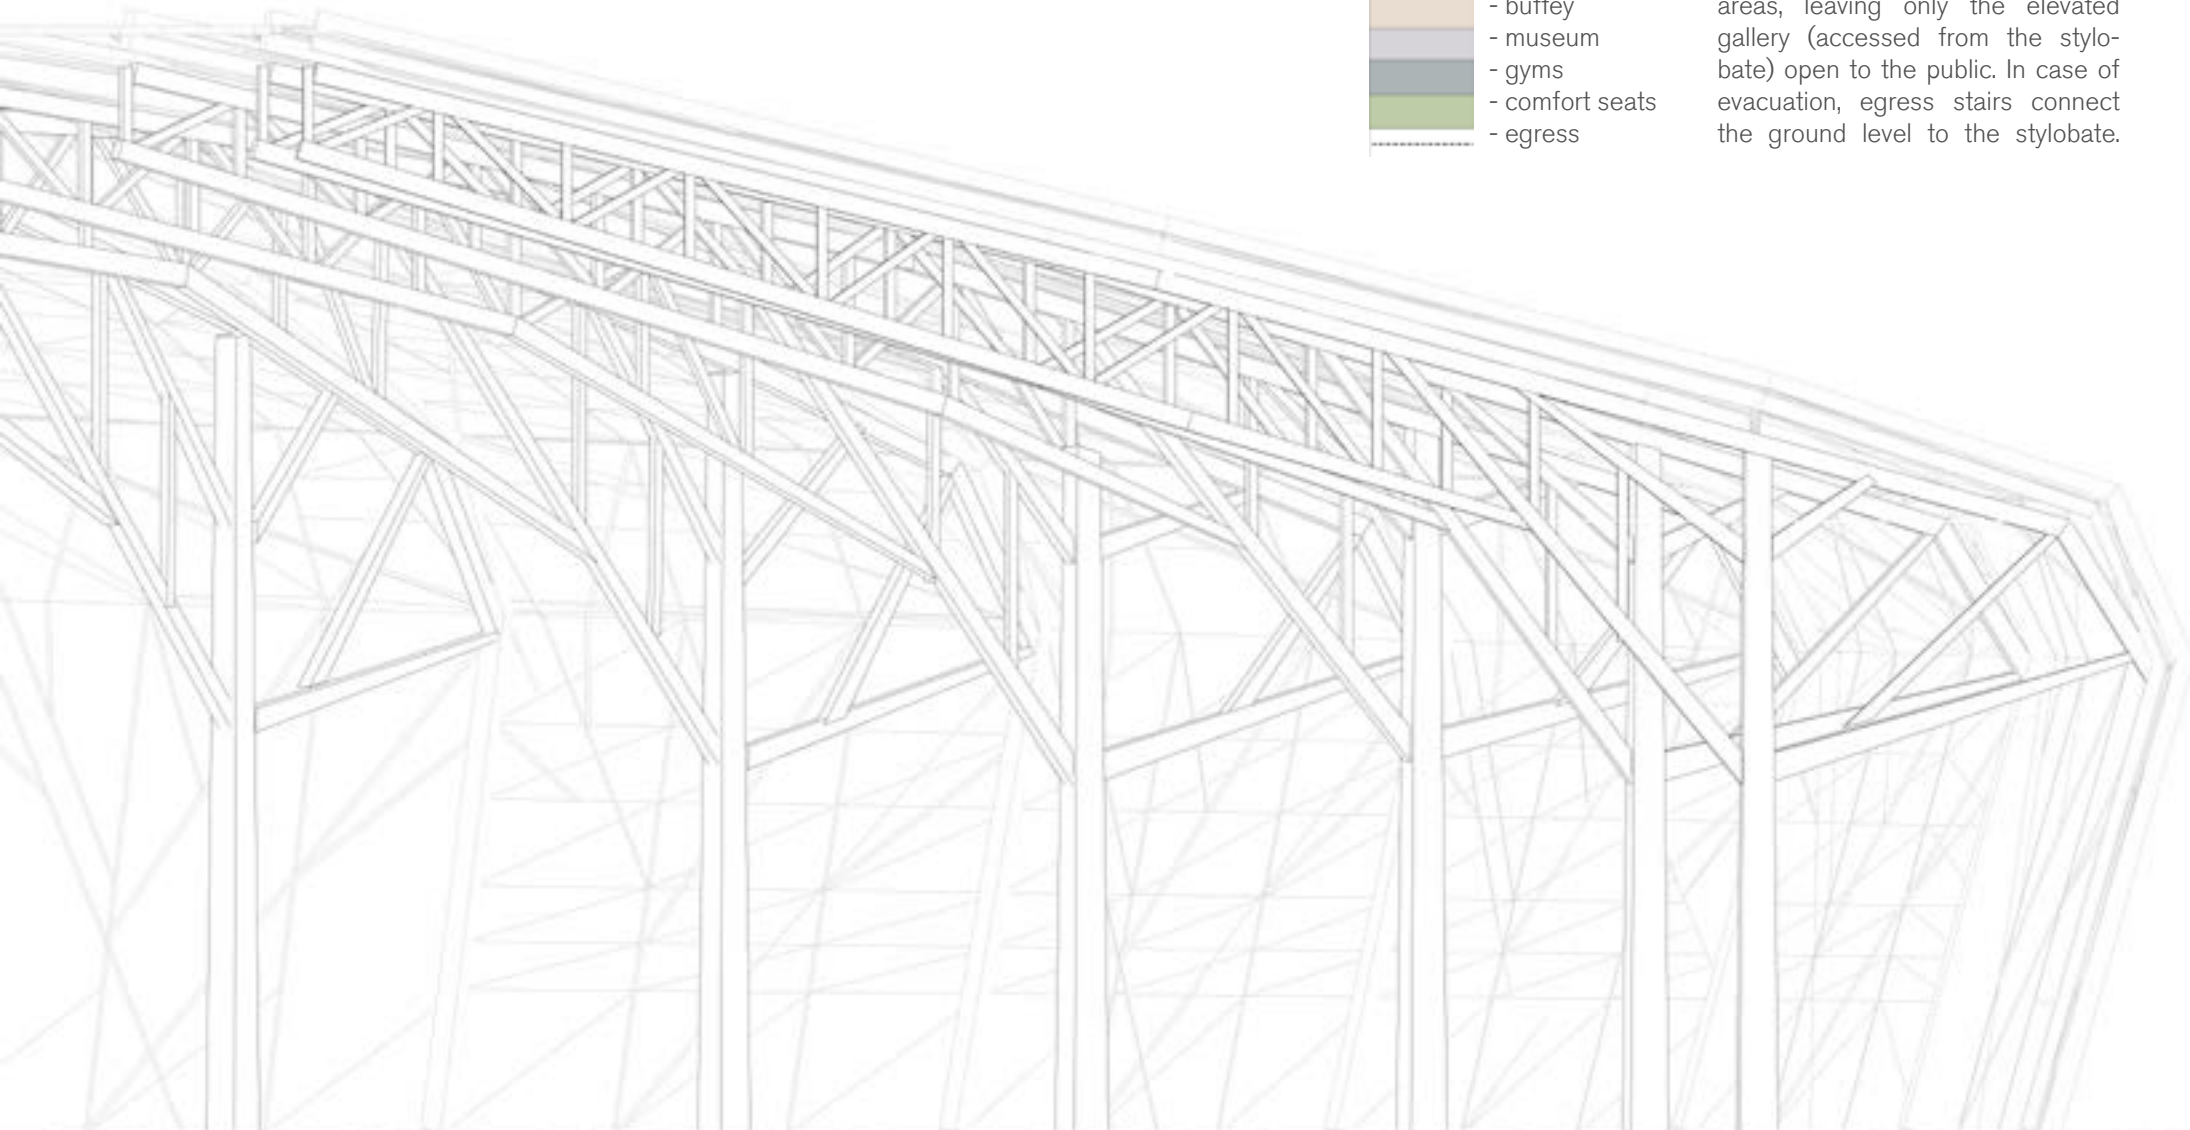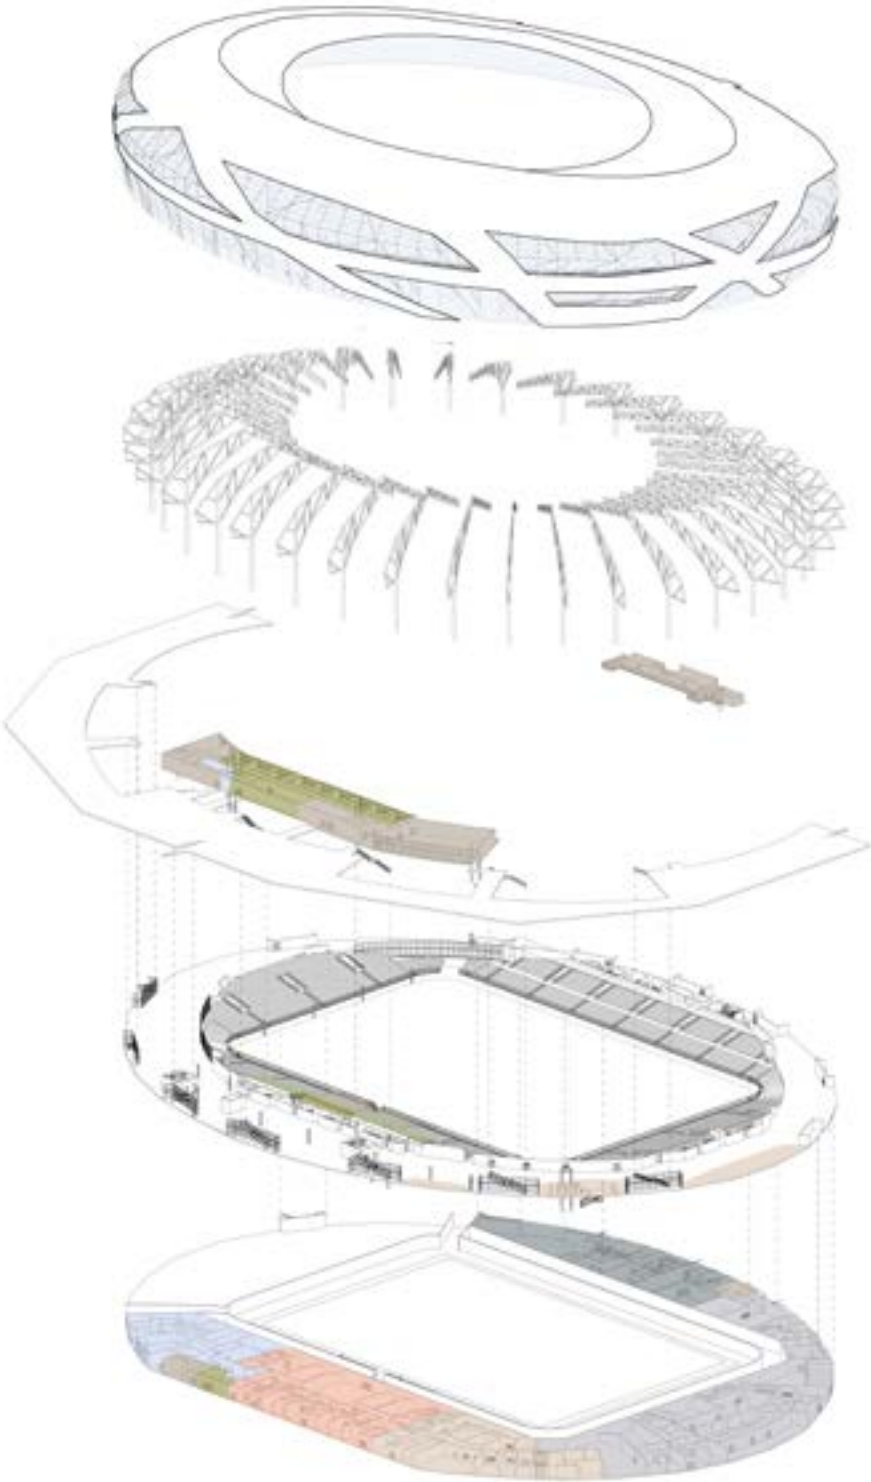

- kitchen zone
- press
- business guests
- players zone
- buffey
- museum
- gyms
- comfort seats
- egress


The perimeter ring of leaning tree-trusses supports the glass facade. All service and support zones are located beneath the seating areas, leaving only the elevated gallery (accessed from the stylobate) open to the public. In case of evacuation, egress stairs connect the ground level to the stylobate.




04 Mariupol Stadium


The stadium competition was part of Mariupol's ambitious urban development in 2020, led by the city as the client. Located in a neglected yet expansive parkland along the Azov Sea in Mariupol, the project aimed to transform a previously unwelcoming area into a vibrant urban destination and a seamless urban connector. The silhouette of the main structure draws inspiration from an asymmetrical pearl. Its flowing curves create a rhythmic presence in the master plan, while the entire composition appears to merge into the surrounding "sea" of trees.



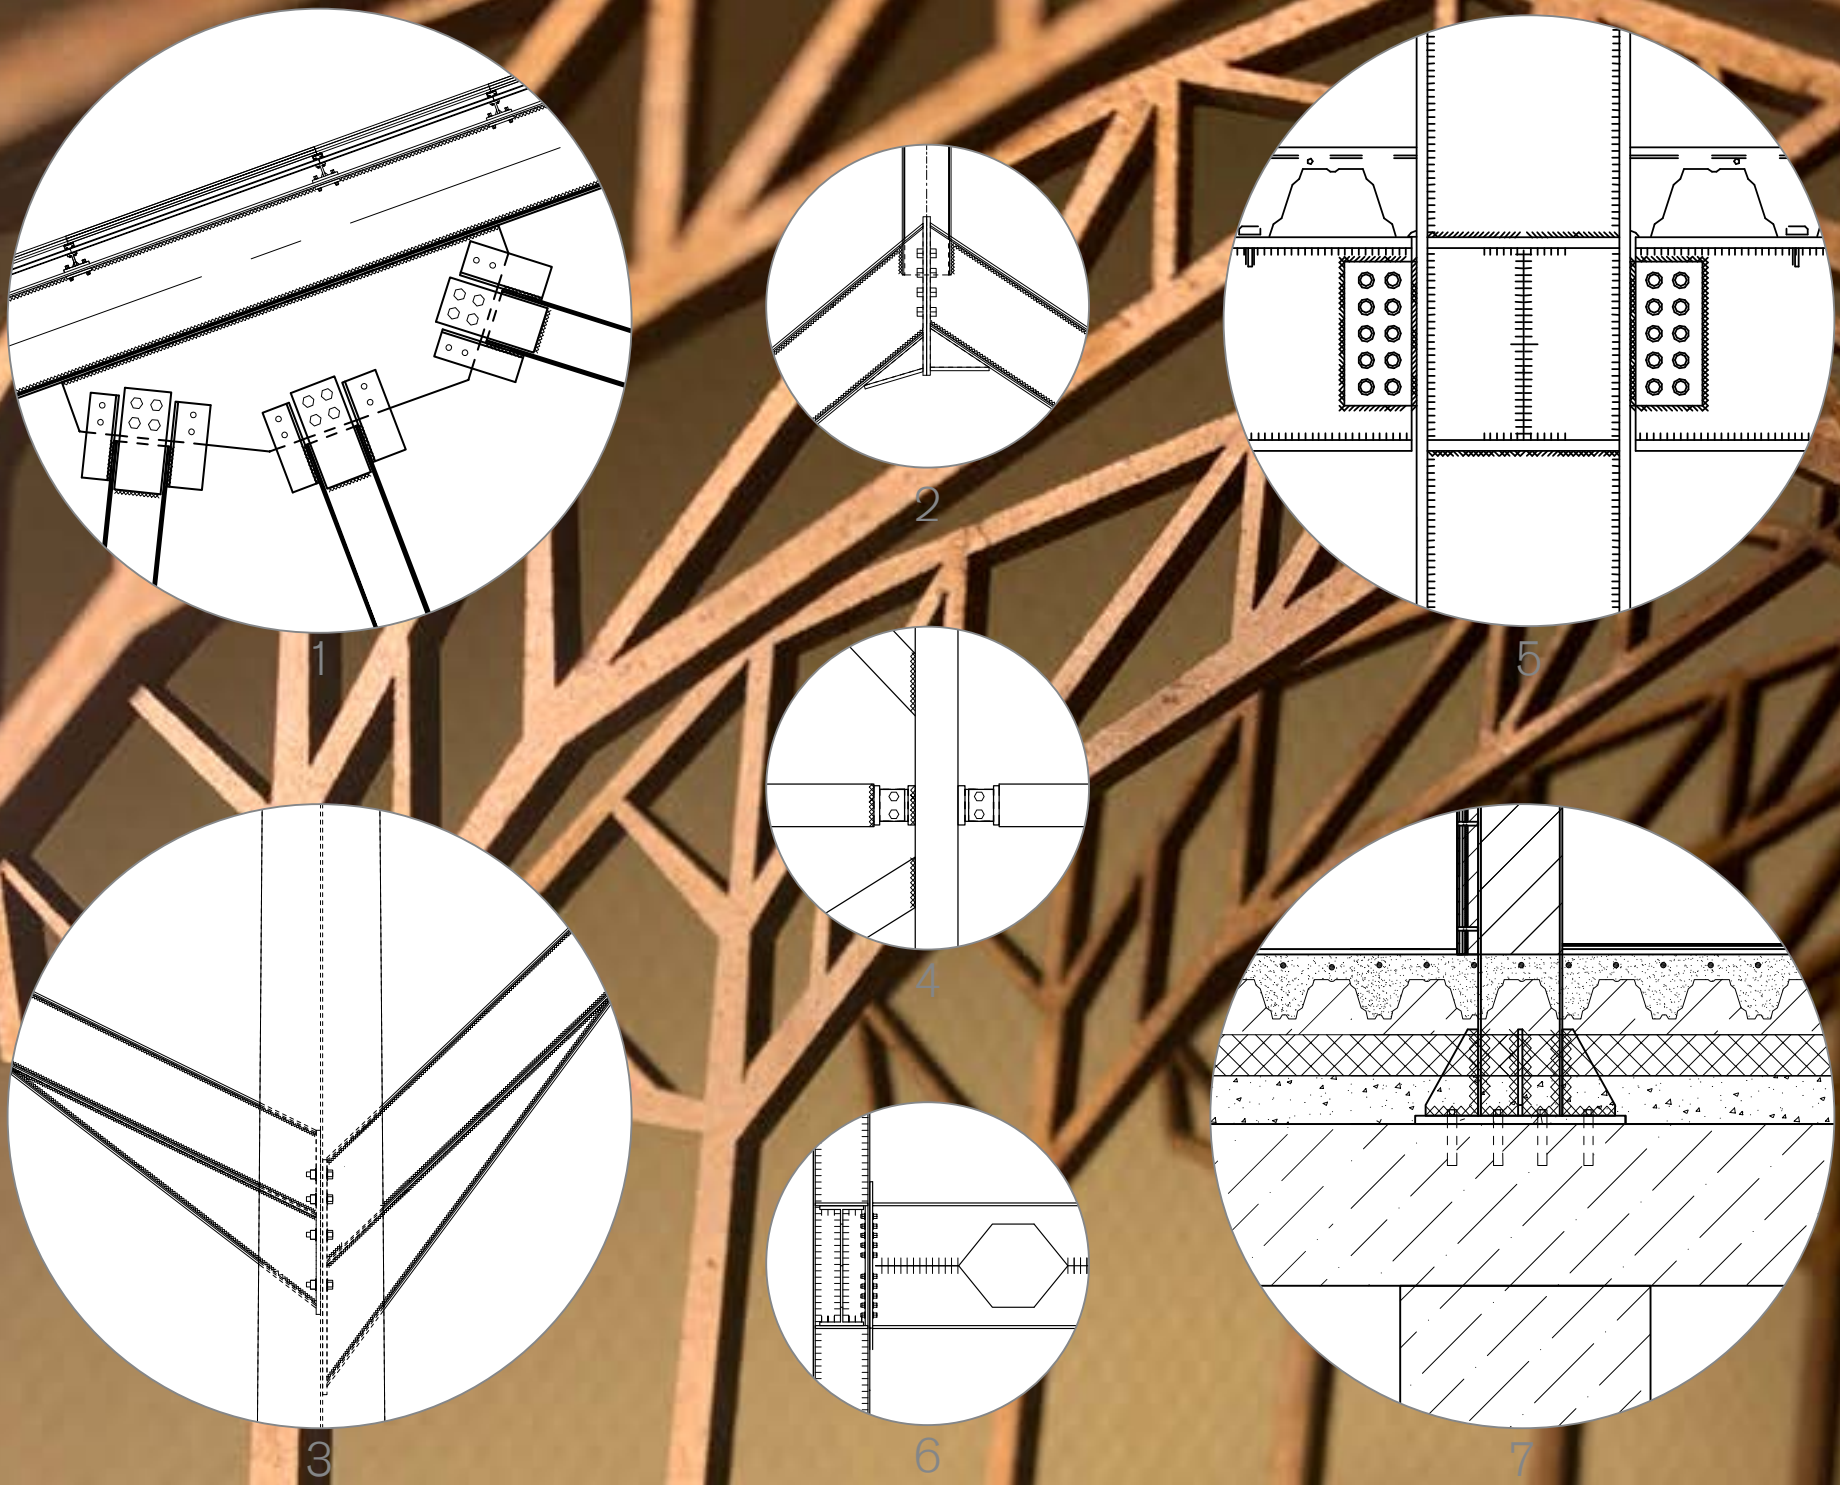

[1] Three webs join where the tree column transitions into the truss, distributing vertical loads into horizontal chords. [2] Two bottom chords meet at a central bearing joint for direct axial load transfer. [3] First-level branches bolted to the web of the H-truss trunk. Triangular gusset plates are inserted for additional support. [4] Shear connection where two tubular webs meet at a central vertical plate. For the indoor structure, [5] in the primary framing, the vertical plates on either side of the stud transfer both axial and bending forces between the built-up beam segments. [6] To reduce the weight, secondary beams are also built-up and have voids. [7] A steel column base is secured to the reinforced concrete foundation with embedded anchor bolts.

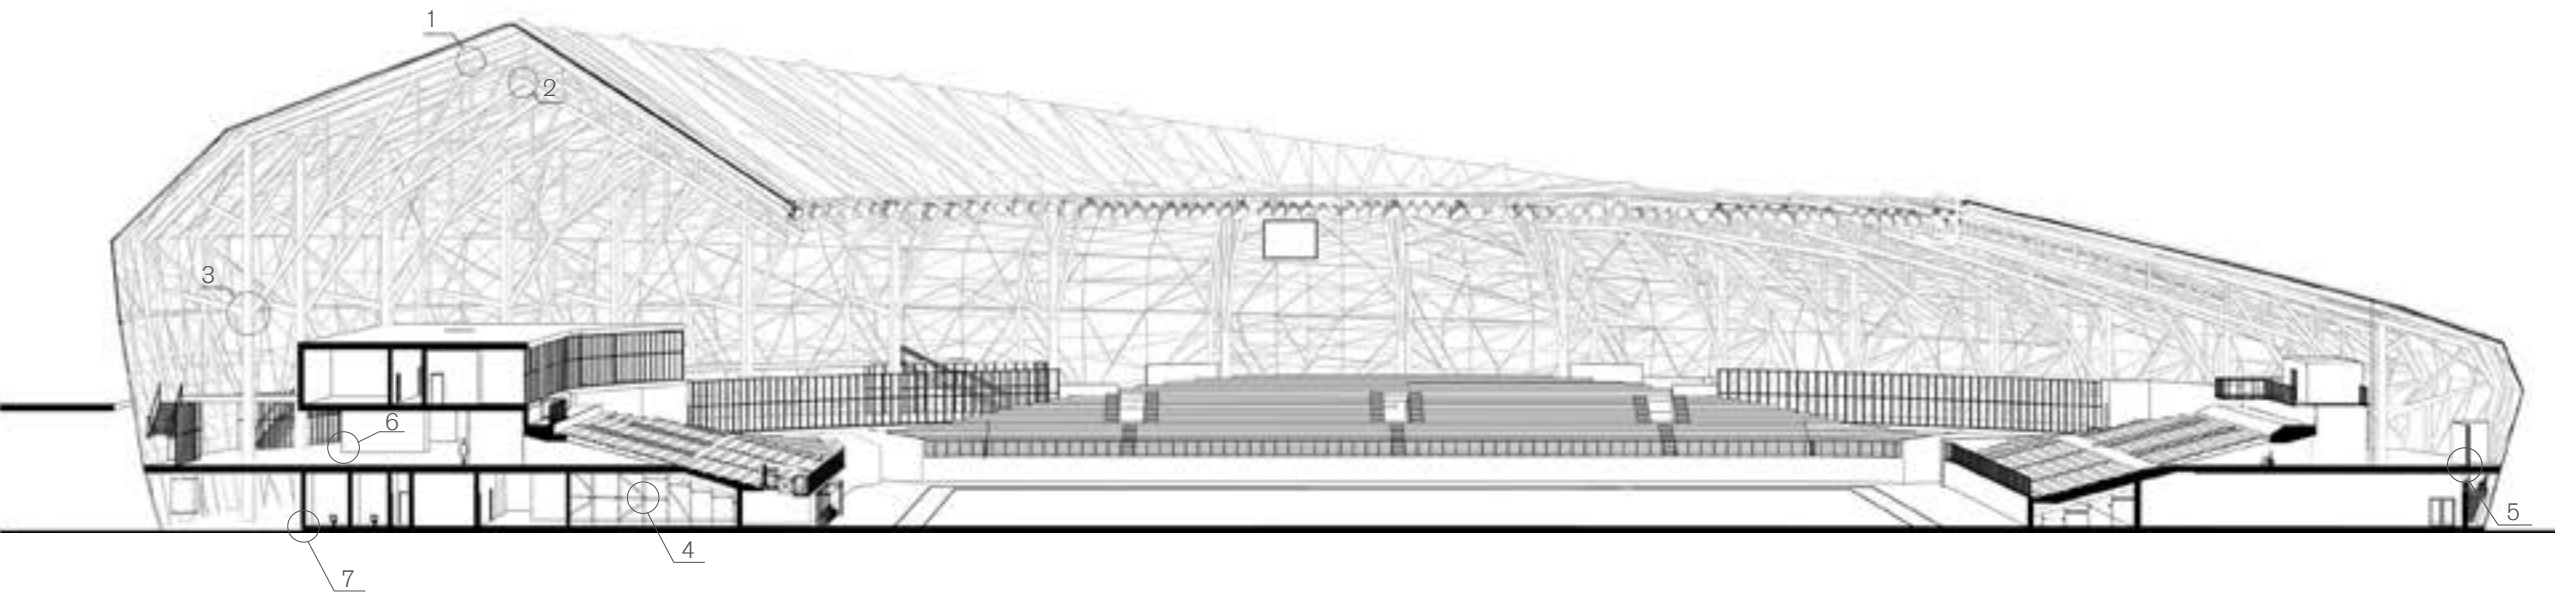

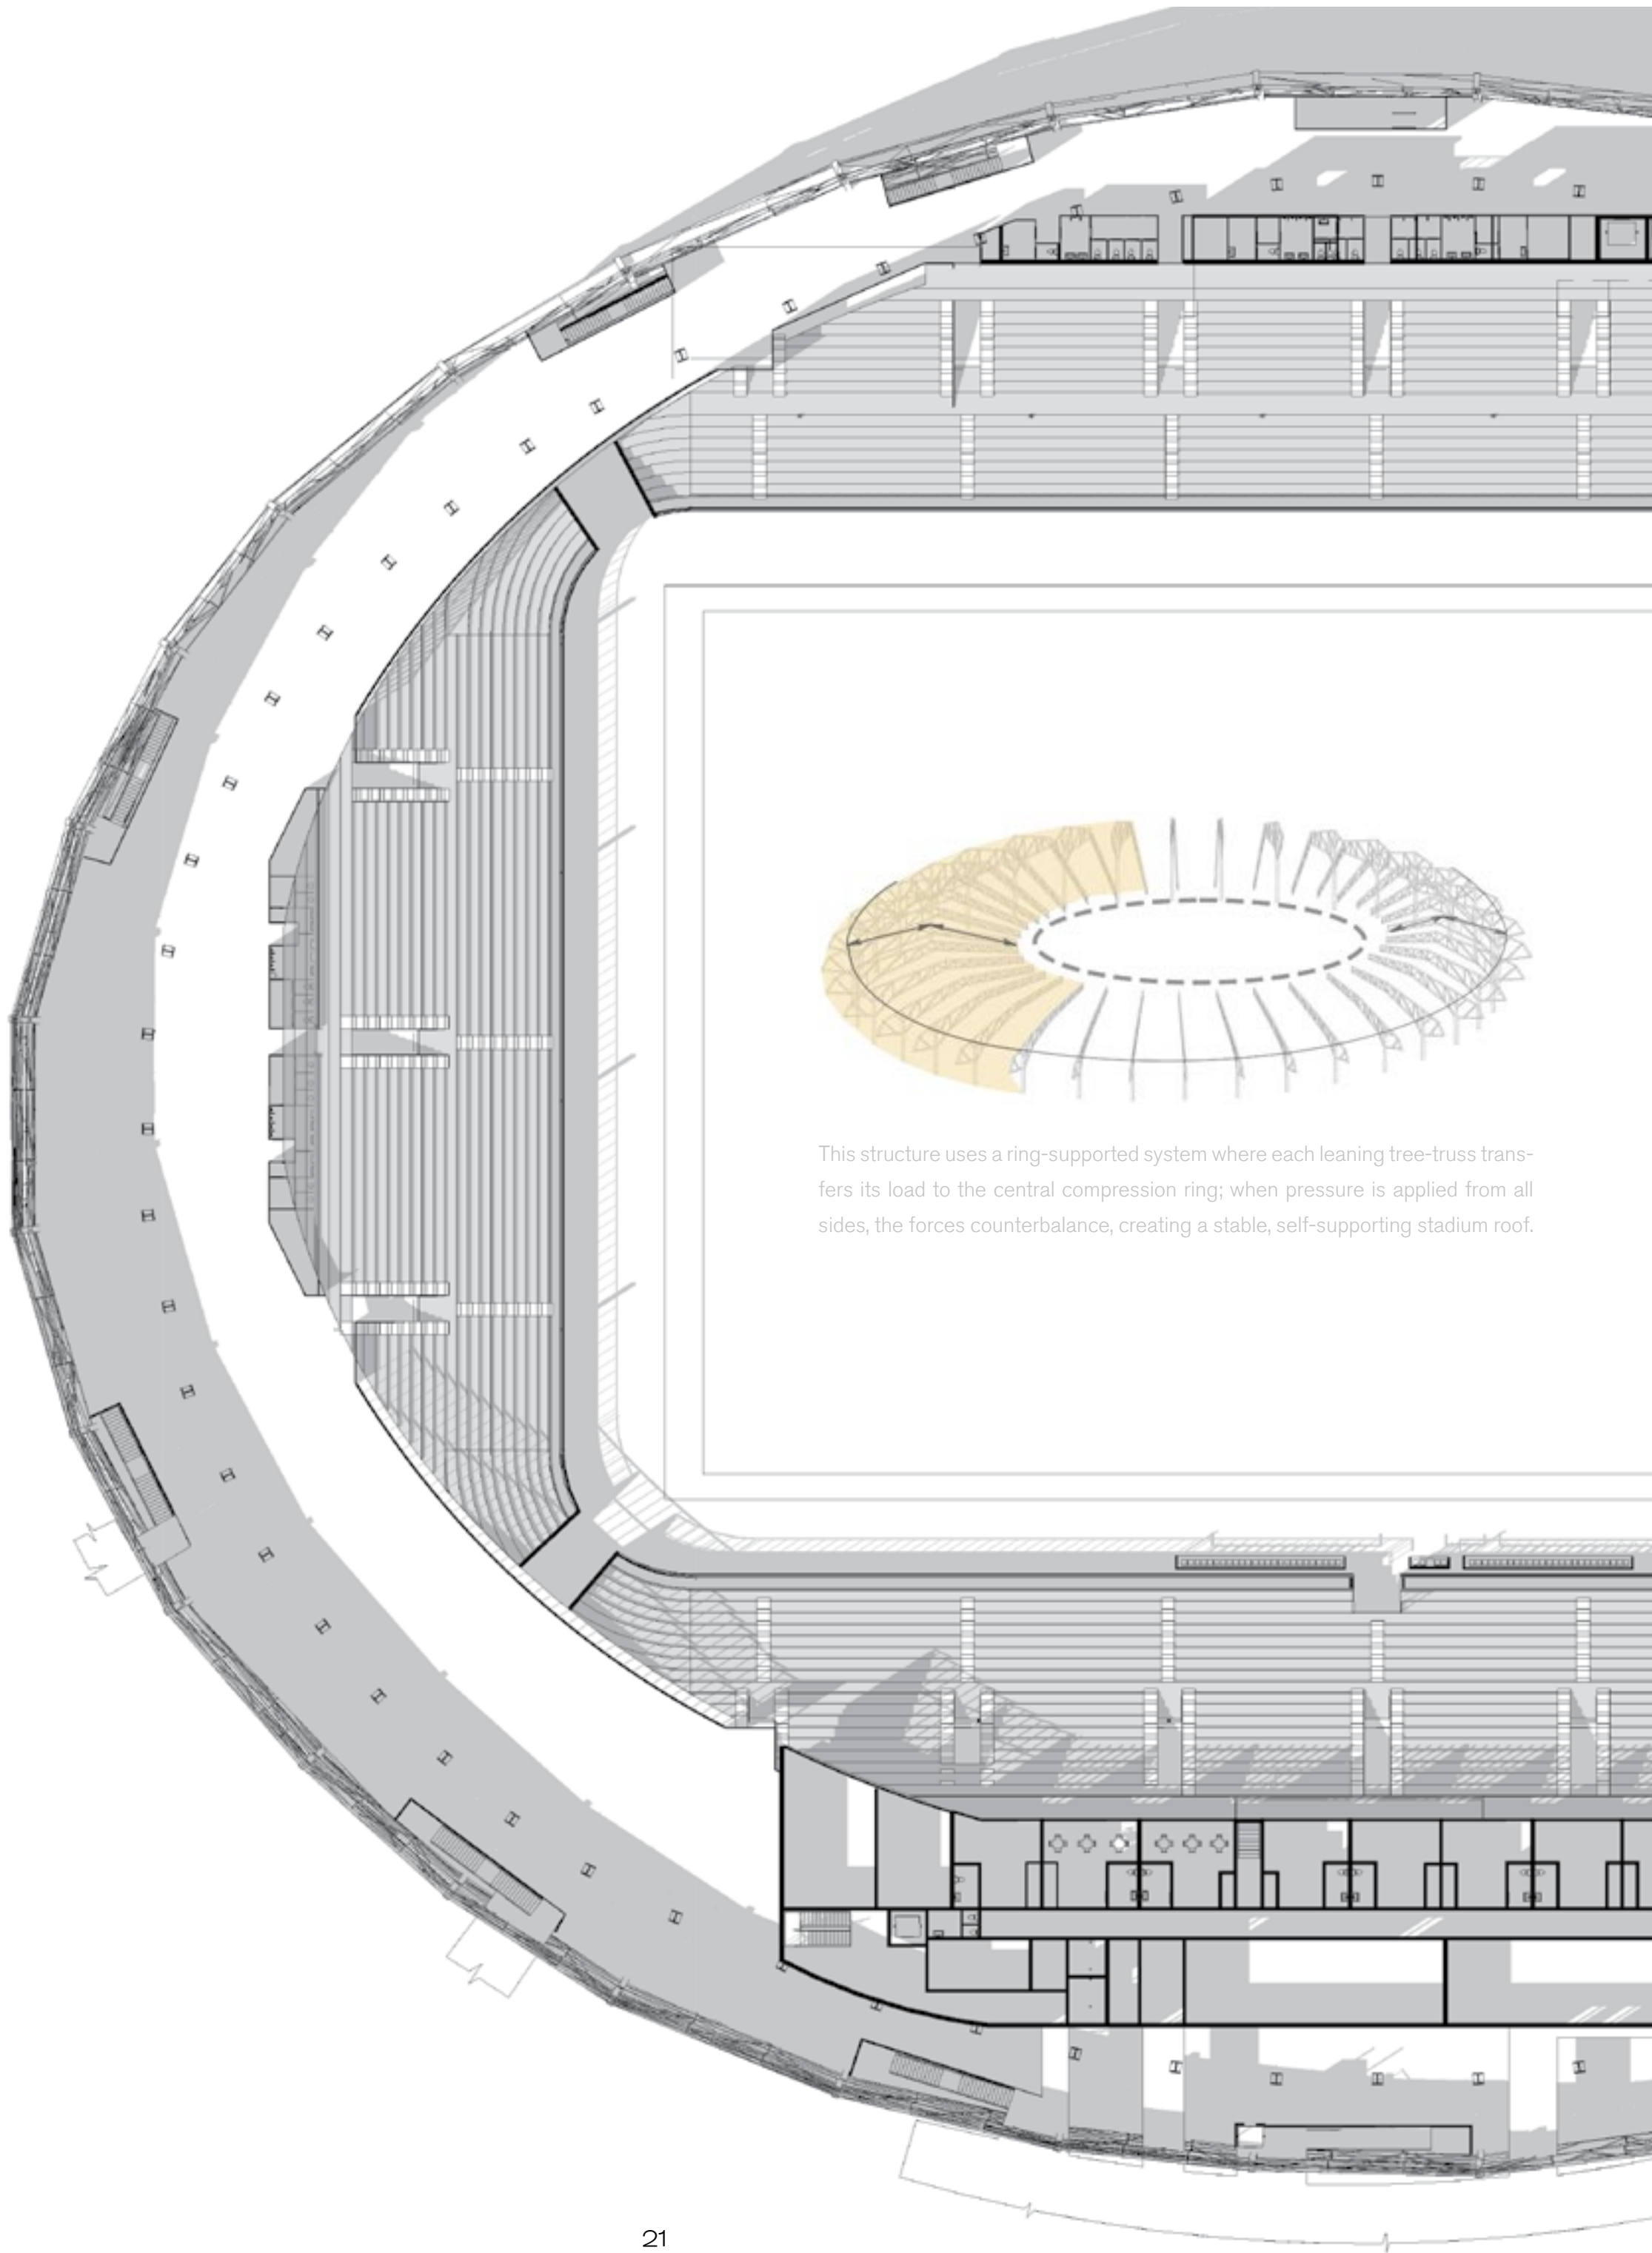

This structure uses a ring-supported system where each leaning tree-truss transfers its load to the central compression ring; when pressure is applied from all sides, the forces counterbalance, creating a stable, self-supporting stadium roof.